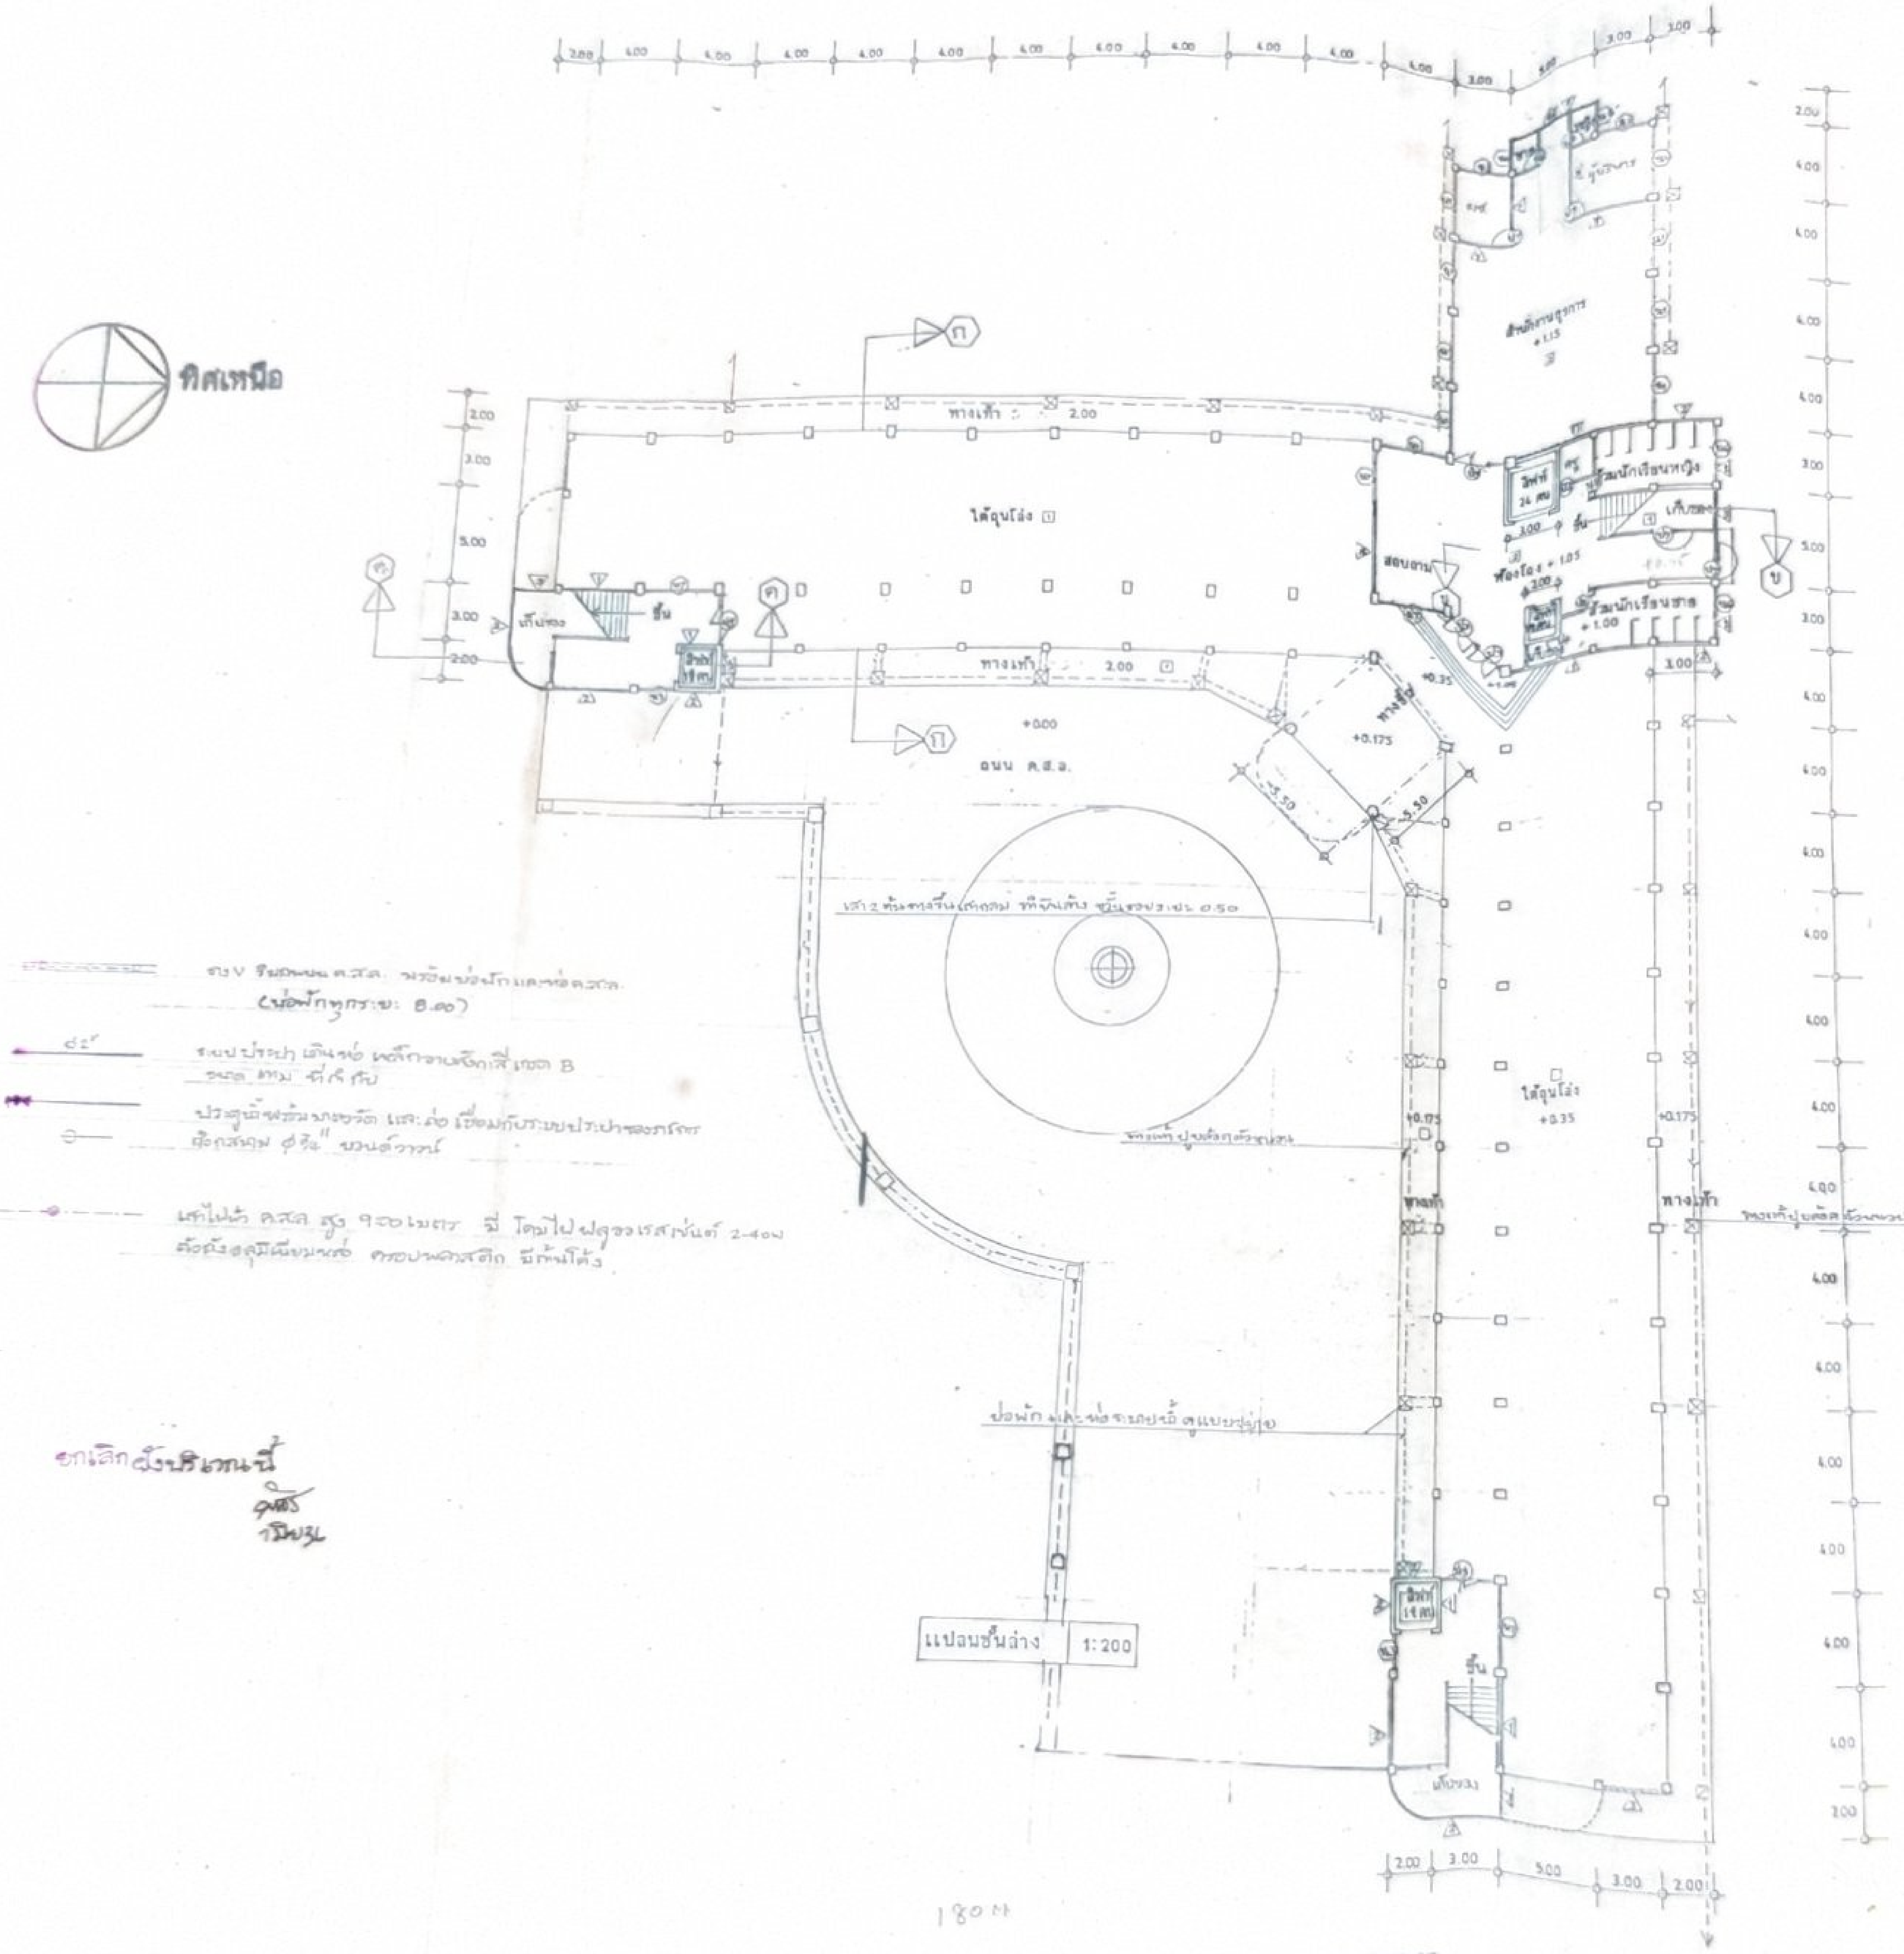
ทิศเหนือ
ทางเท้า 2.00
ใต้ถุนโล่ง
ใต้ถุนโล่ง +0.35
ถนน ค.ส.ล.
+0.00
+0.175
ทางเท้า
สอบถาม
ห้องโถง +1.05
ห้องน้ำนักเรียนหญิง
ห้องน้ำนักเรียนชาย +1.00
เก็บของ
ลิฟท์ 24 คน
ลิฟท์ 14 คน
ขึ้น
+1.15
แปลนชั้นล่าง 1:200
2.00
3.00
4.00
5.00

ราง V ริมถนน ค.ส.ล. พร้อมบ่อพักและท่อ ค.ส.ล.
(บ่อพักทุกระยะ 8.00)

ระบบประปา เดินท่อ เหล็กอาบสังกะสี เกรด B
ขนาด ตาม ที่กำหนด

ประตูน้ำพร้อมมาตรวัด และ ต่อ เชื่อมกับระบบประปาของภูมิภาค
[illegible] ๔ นิ้ว [illegible]

เสาไฟฟ้า ค.ส.ล. สูง 9.00 เมตร มี โคมไฟฟลูออเรสเซ้นต์ 2-40W
ตัวถังอลูมิเนียมหล่อ ครอบพลาสติก มีก้านโค้ง

ยกเลิกตั้งบริเวณนี้

180ม

หมายเหตุ
ใช้สำหรับงานก่อสร้างของ

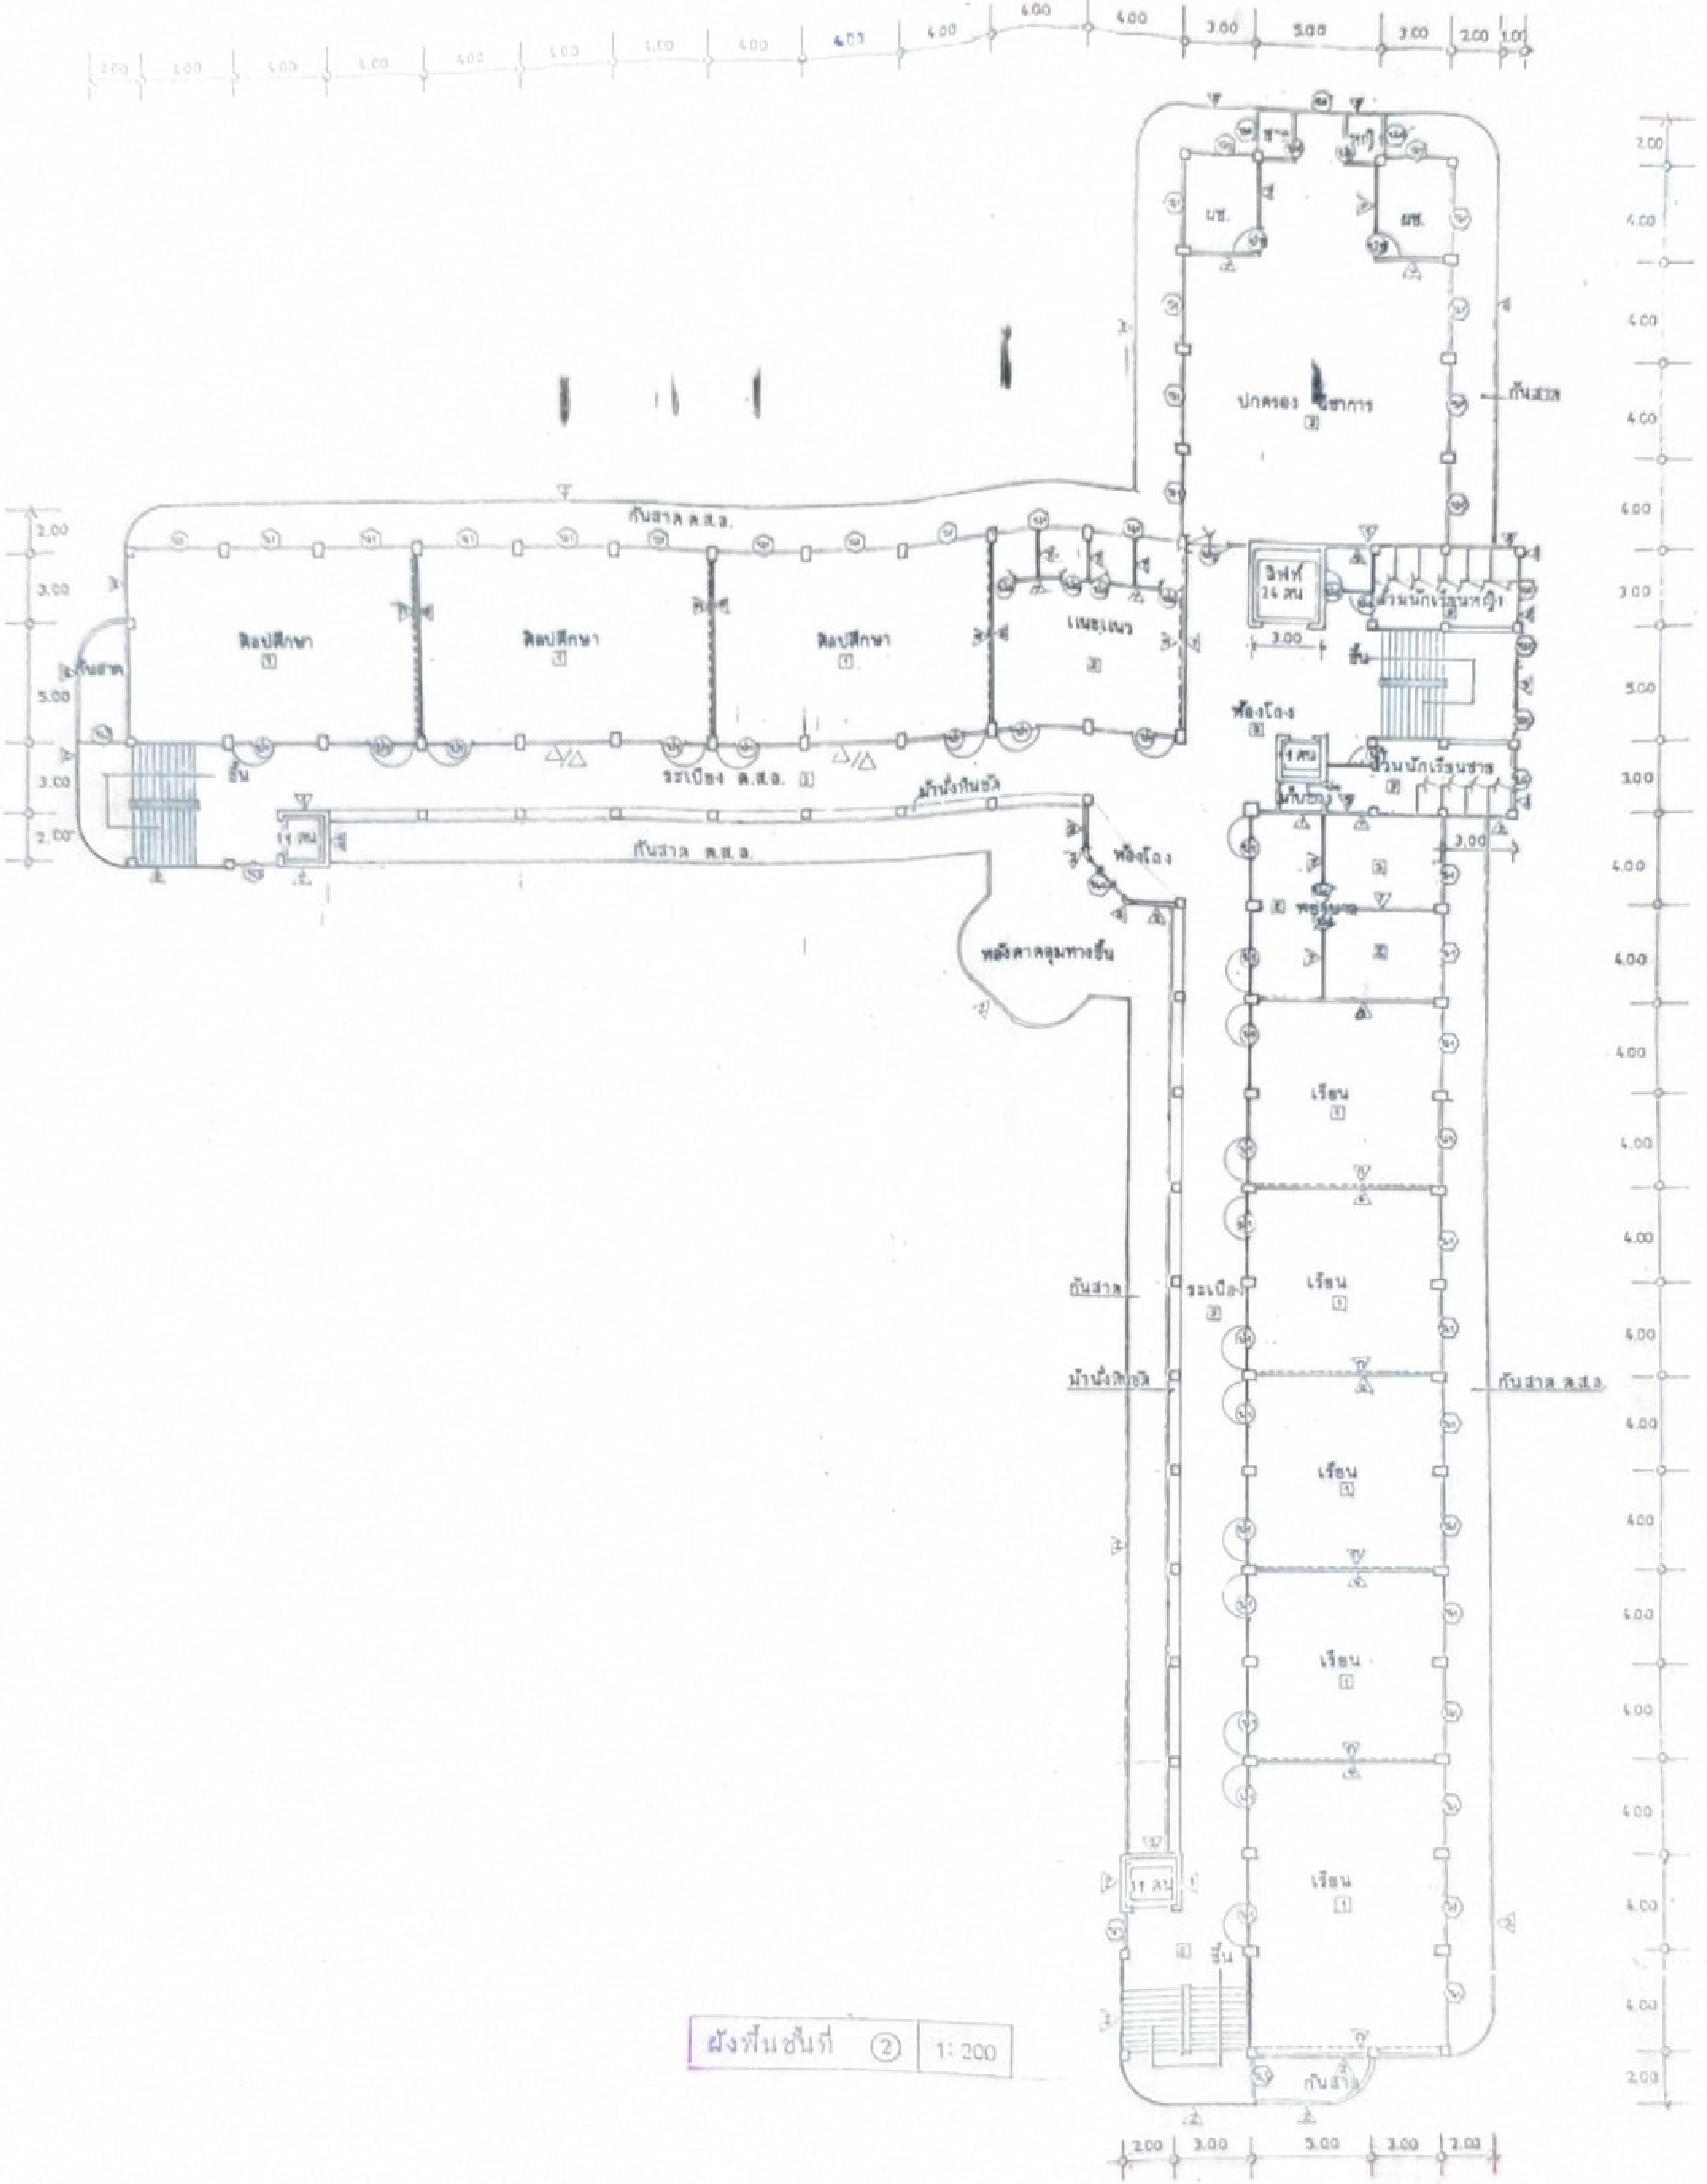
2.00
4.00
4.00
4.00
4.00
4.00
4.00
4.00
4.00
4.00
4.00
4.00
3.00
5.00
3.00
2.00
1.00
ผช.
ผญ.
ปกครอง วิชาการ
กันสาด
กันสาด ค.ส.ล.
ศิลปศึกษา
ศิลปศึกษา
ศิลปศึกษา
แนะแนว
ลิฟท์ 24 คน
ส้วมนักเรียนหญิง
3.00
ขึ้น
ห้องโถง
4 คน
ส้วมนักเรียนชาย
ระเบียง ค.ส.ล.
ม้านั่งกันตัว
15 คน
กันสาด ค.ส.ล.
ห้องโถง
หลังคาคลุมทางขึ้น
พยาบาล
3.00
เรียน
เรียน
เรียน
เรียน
เรียน
กันสาด
ระเบียง
ม้านั่งกันตัว
กันสาด ค.ส.ล.
ขึ้น
15 คน
กันสาด
2.00
3.00
5.00
3.00
2.00

ผังพื้นชั้นที่ ② 1:200

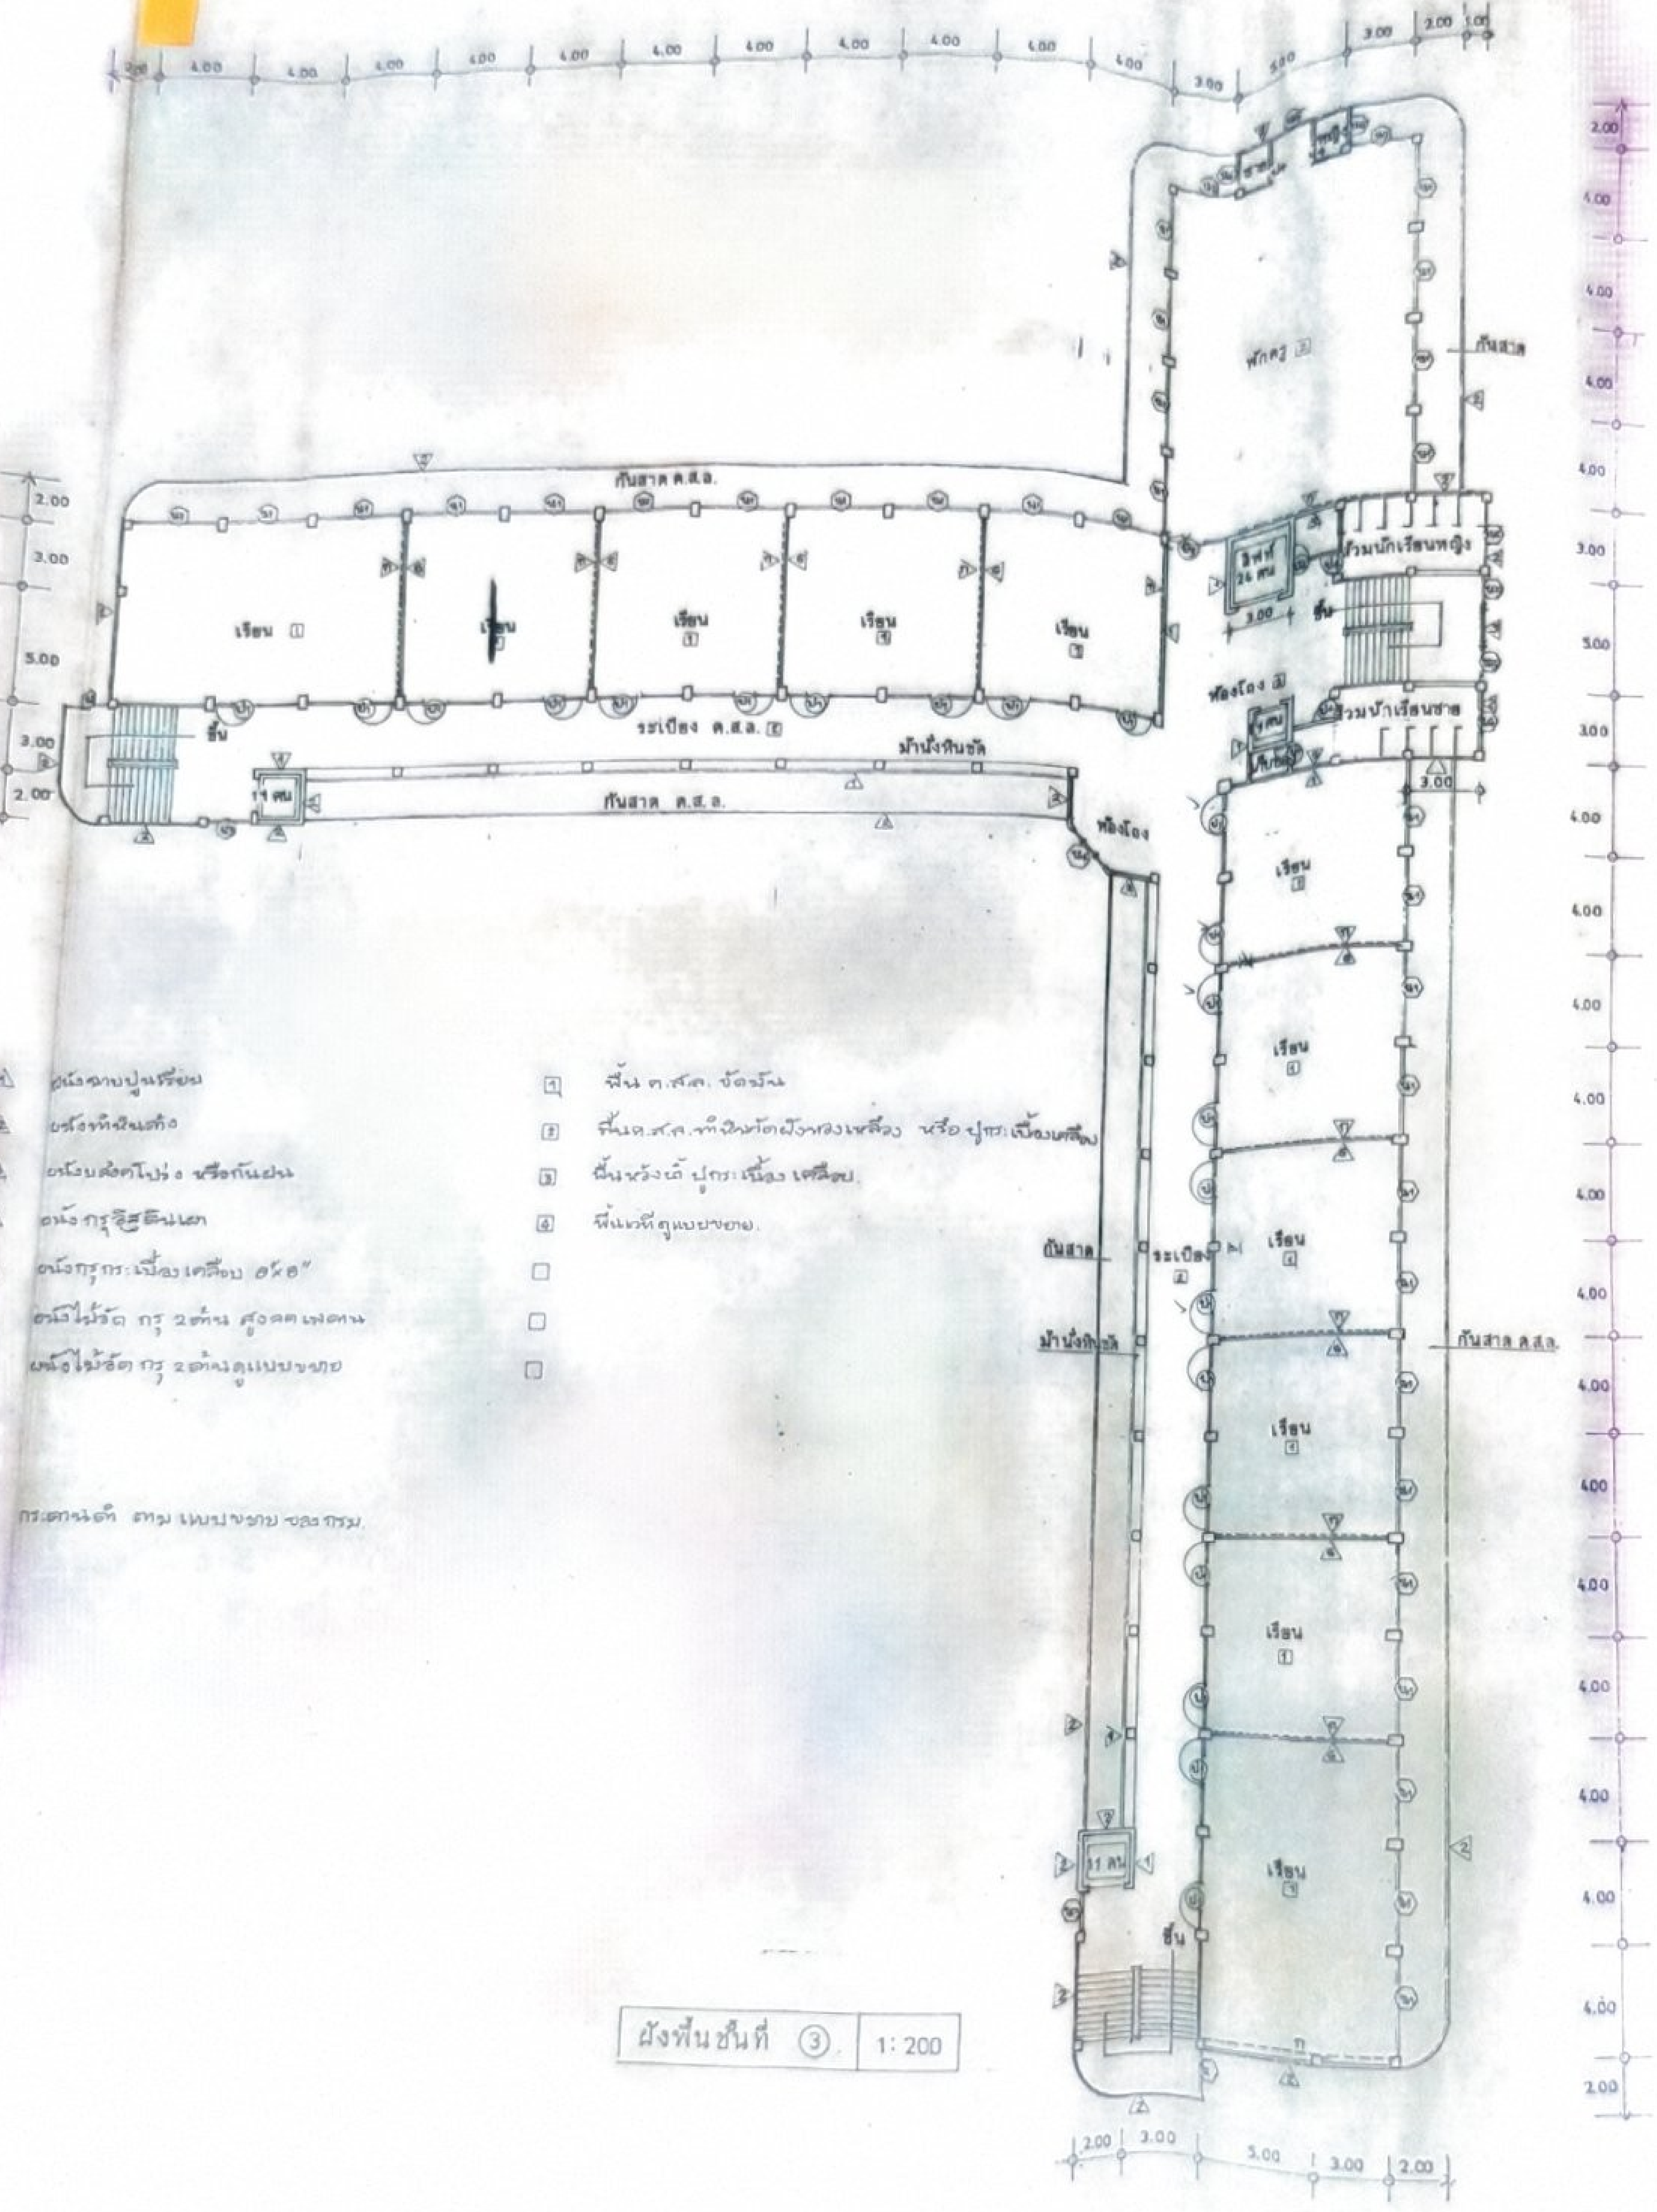
ผังพื้นชั้นที่ ③ 1:200
เรียน
พักครู
กันสาด
กันสาด ค.ส.ล.
ระเบียง ค.ส.ล.
ม้านั่งหินขัด
ลิฟท์ 24 คน
ส้วมนักเรียนหญิง
ส้วมนักเรียนชาย
ห้องโถง
ขึ้น
11 คน
1 ผนังฉาบปูนเรียบ
2 ผนังทำหินล้าง
3 ผนังบล็อคโปร่ง หรือกันฝน
4 ผนังกรุอิฐดินเผา
5 ผนังกรุกระเบื้องเคลือบ 6×6"
6 ผนังไม้อัด กรุ 2ด้าน สูงจดเพดาน
7 ผนังไม้อัด กรุ 2ด้านดูแบบขยาย
A กระดานดำ ตามแบบขยาย ของกรม
1 พื้น ค.ส.ล. ขัดมัน
2 พื้น ค.ส.ล. ทำผิวหินขัดฝังทองเหลือง หรือ ปูกระเบื้องเคลือบ
3 พื้นห้องน้ำ ปูกระเบื้องเคลือบ
4 พื้นเวทีดูแบบขยาย
2.00
4.00
3.00
5.00

หมายเหตุ

ใช้สำหรับงานก่อสร้างของ
โรงเรียนสวนกุหลาบวิทยาลัย รังสิต
ปี 2536

เมย36

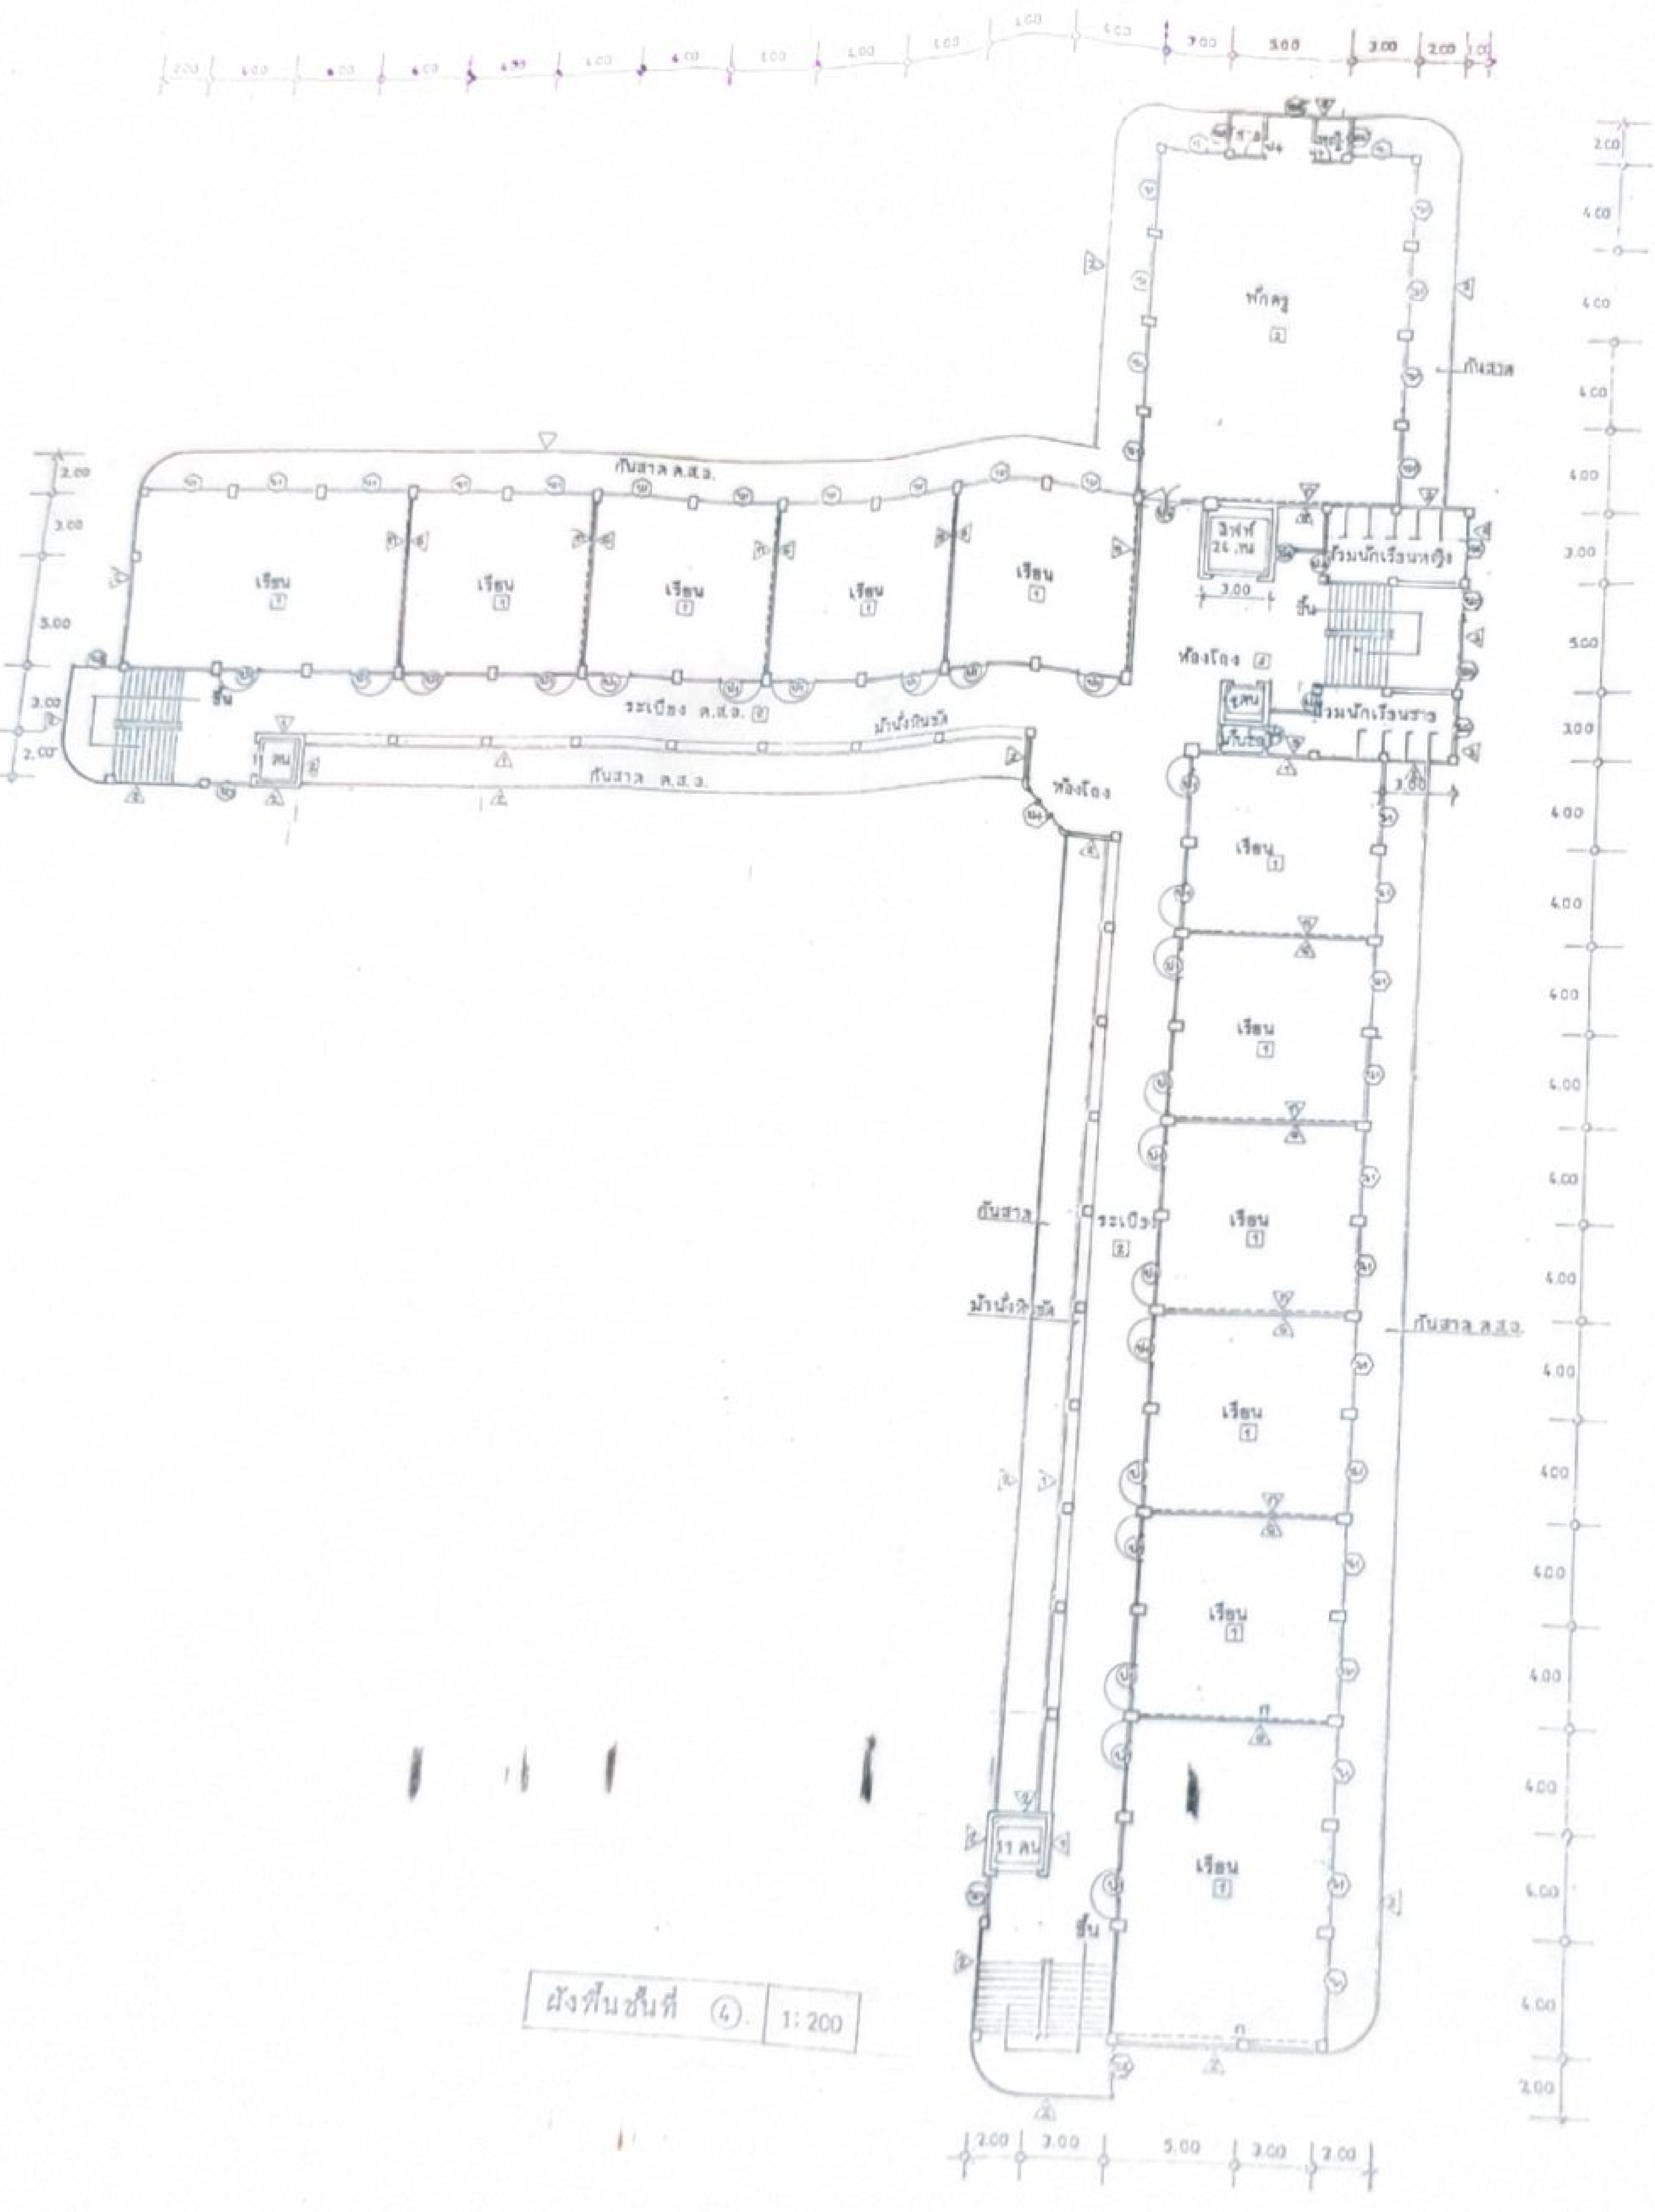
พักครู
กันสาด
กันสาด ค.ส.ล.
เรียน
ลิฟท์ 24 คน
ส้วมนักเรียนหญิง
ขึ้น
ห้องโถง
ส้วมนักเรียนชาย
ระเบียง ค.ส.ล.
ม้านั่งกันตก
ลิฟท์ 11 คน
ระเบียง
3.00
2.00
5.00
4.00

ผังพื้นชั้นที่ ④ 1:200

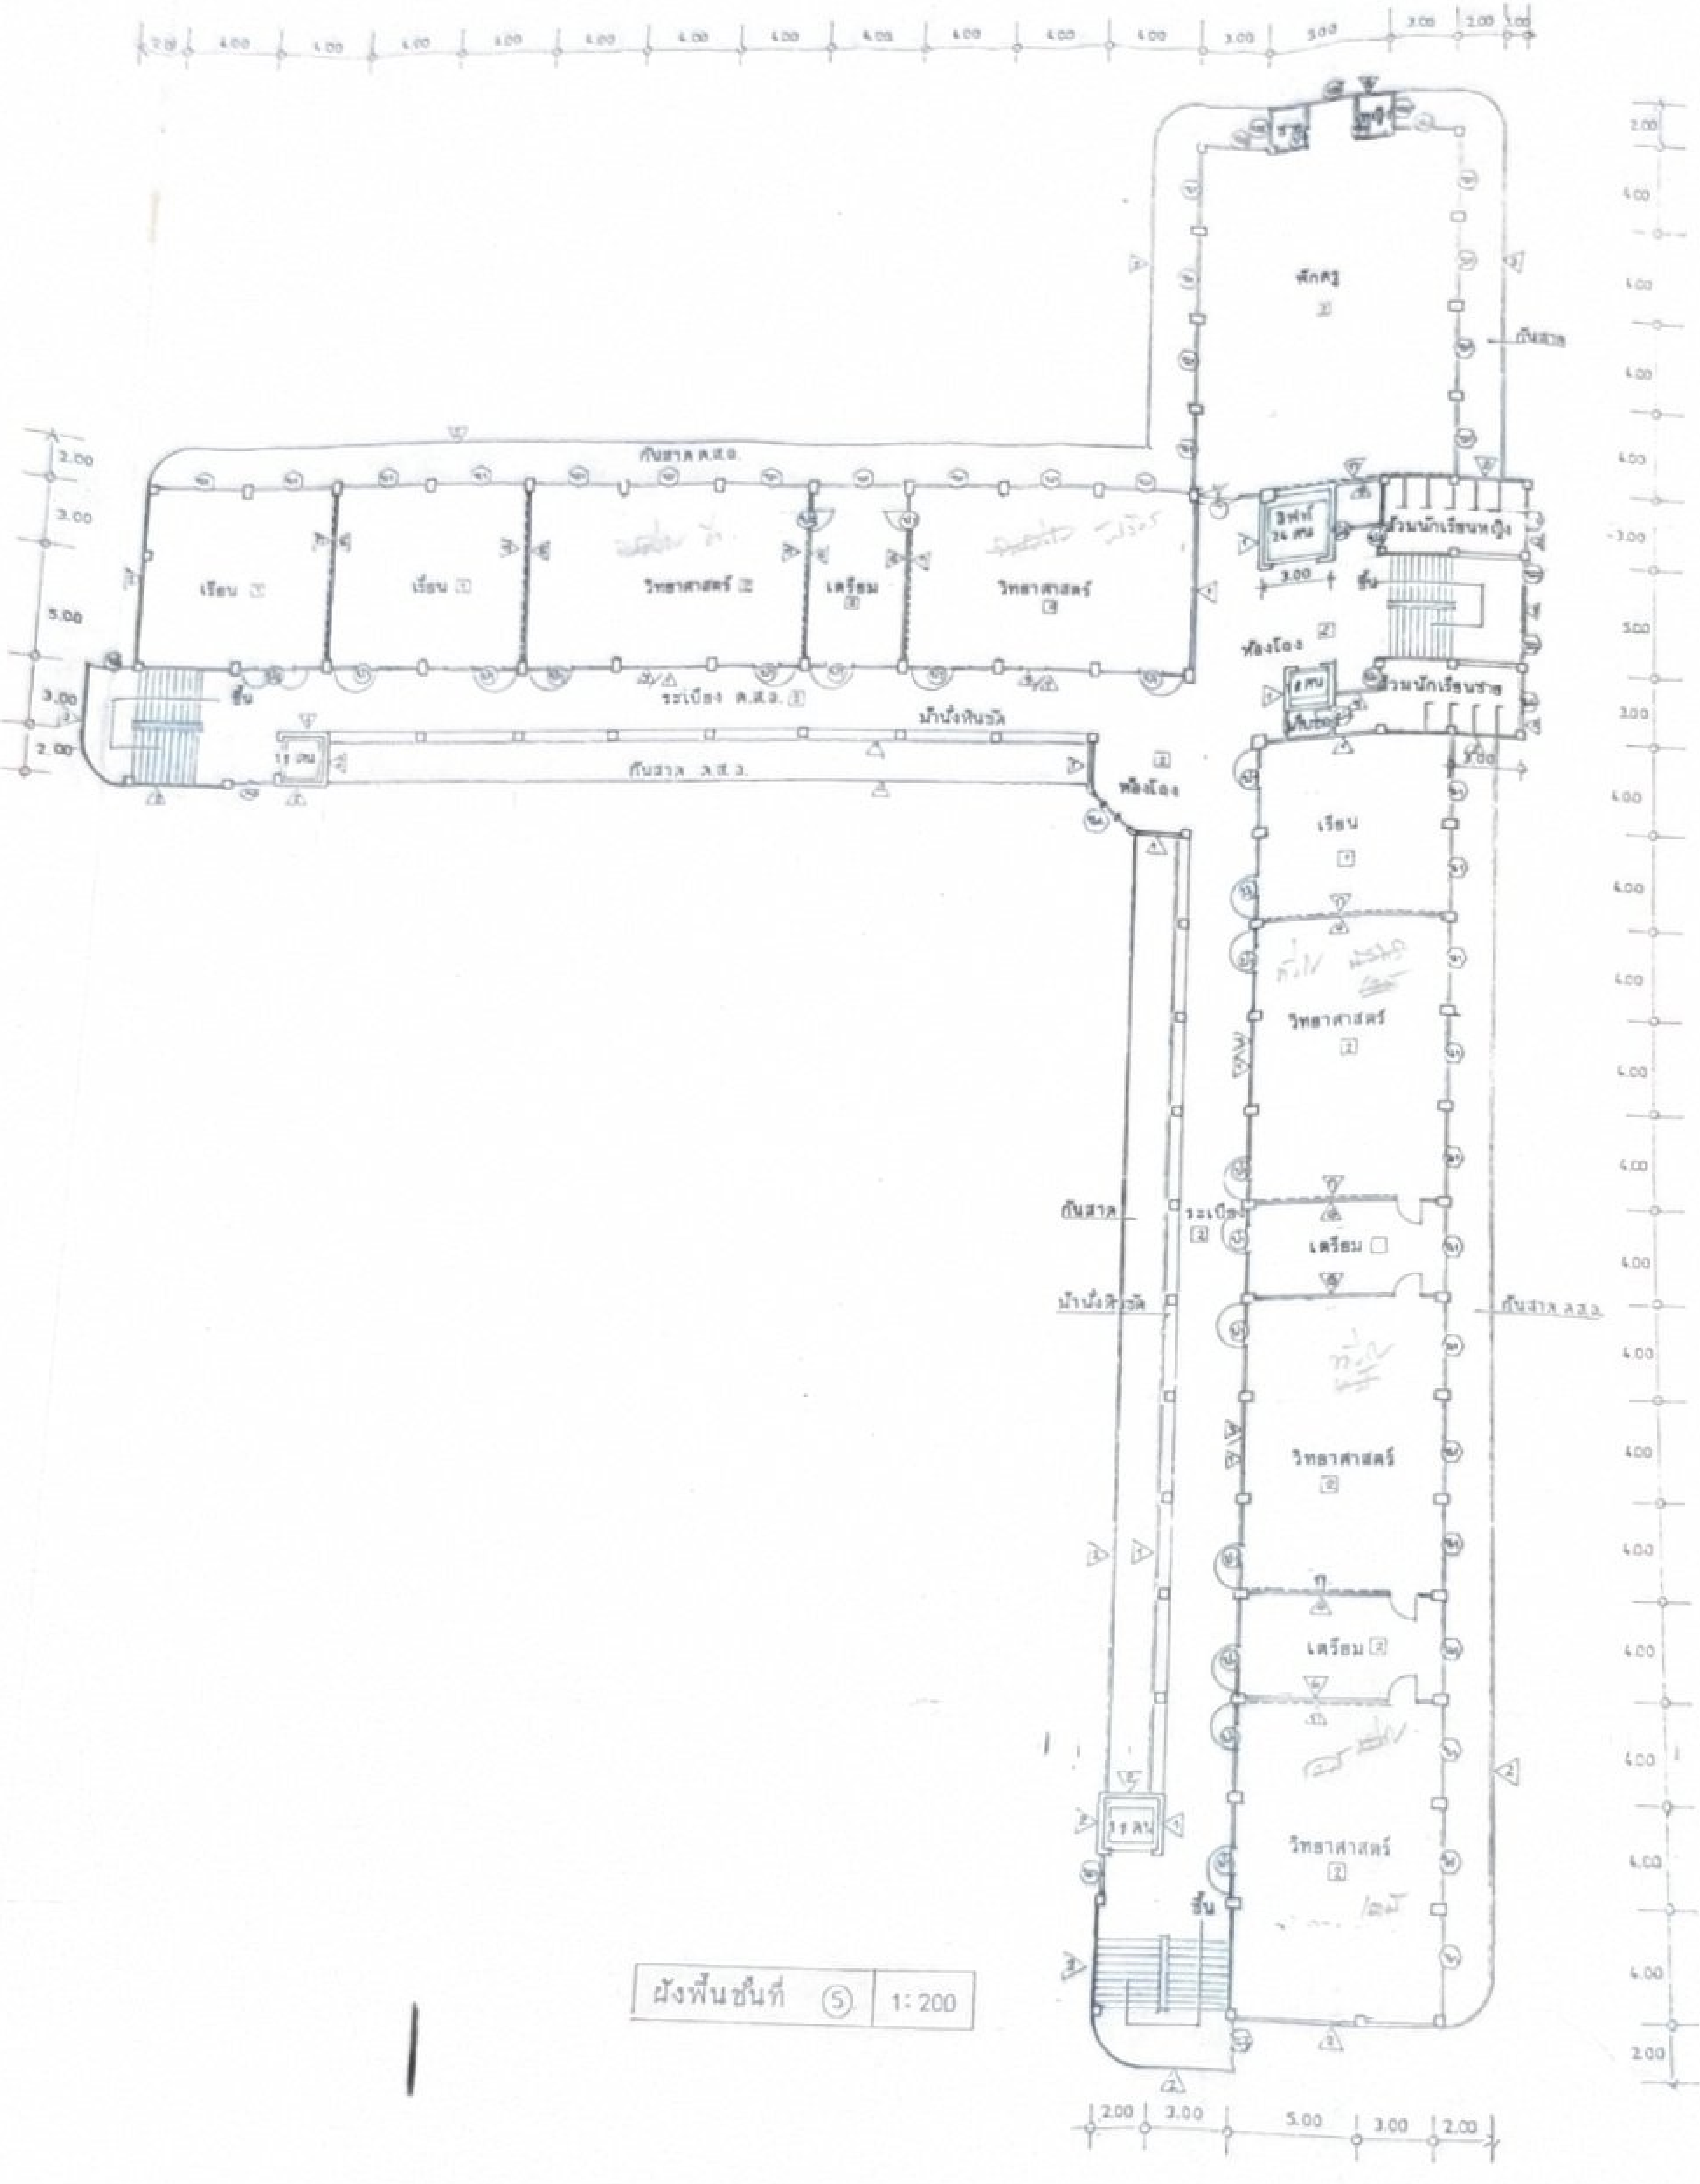
พักครู
กันสาด
กันสาด ค.ส.ล.
เรียน
วิทยาศาสตร์
เตรียม
ลิฟท์ 24 คน
ส้วมนักเรียนหญิง
ส้วมนักเรียนชาย
ขึ้น
ห้องโถง
ระเบียง ค.ส.ล.
ม้านั่งหินขัด
11 คน
ระเบียง
2.00
3.00
4.00
5.00

ผังพื้นชั้นที่ ⑤ 1: 200

หมายเหตุ
ใช้สำหรับงานก่อสร้างของ
โรงเรียนสวนกุหลาบวิทยาลัย รังสิต
ปี 2536

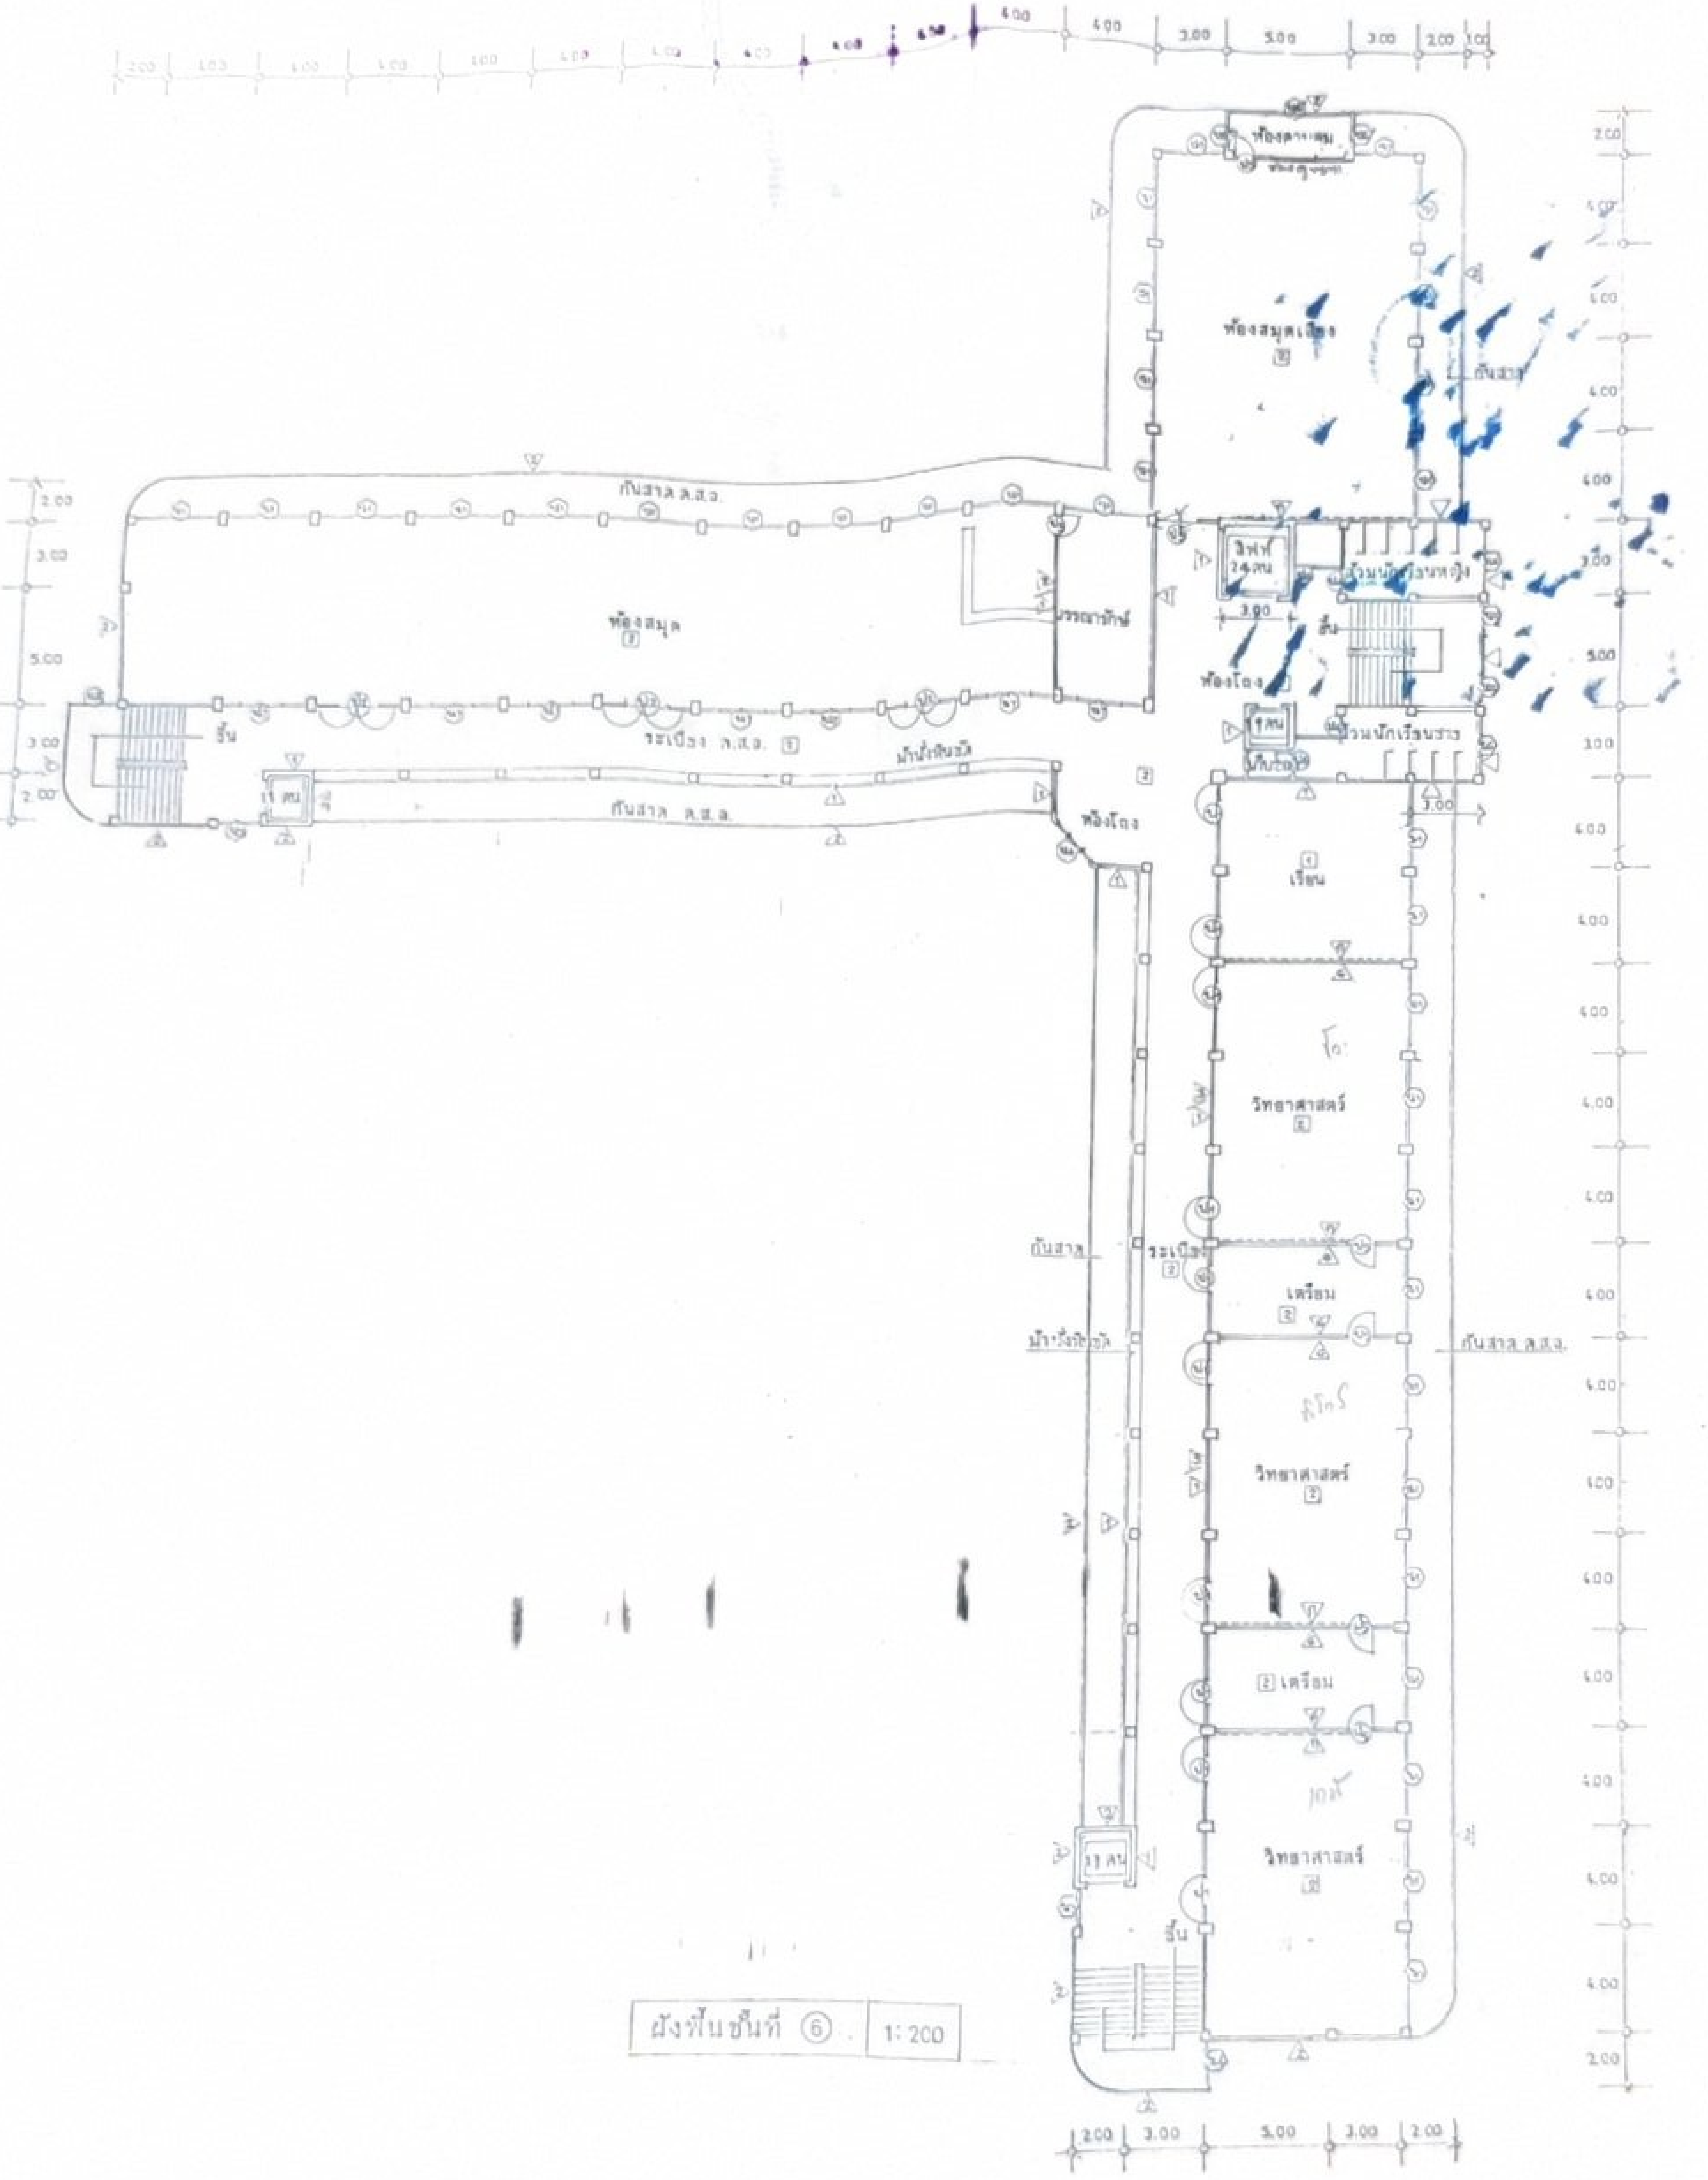
ห้องสมุดเสียง
กันสาด
ลิฟท์ 24 คน
3.00
ส้วมนักเรียนหญิง
ขึ้น
ห้องโถง
11 คน
ส้วมนักเรียนชาย
เก็บของ
กันสาด ค.ส.ล.
ห้องสมุด
บรรณารักษ์
ระเบียง ค.ส.ล.
ม้านั่งหินขัด
ห้องโถง
เรียน
วิทยาศาสตร์
เตรียม
ระเบียง
กันสาด
ม้านั่งหินขัด
กันสาด ค.ส.ล.
2.00
3.00
4.00
5.00

ผังพื้นชั้นที่ ⑥ 1:200

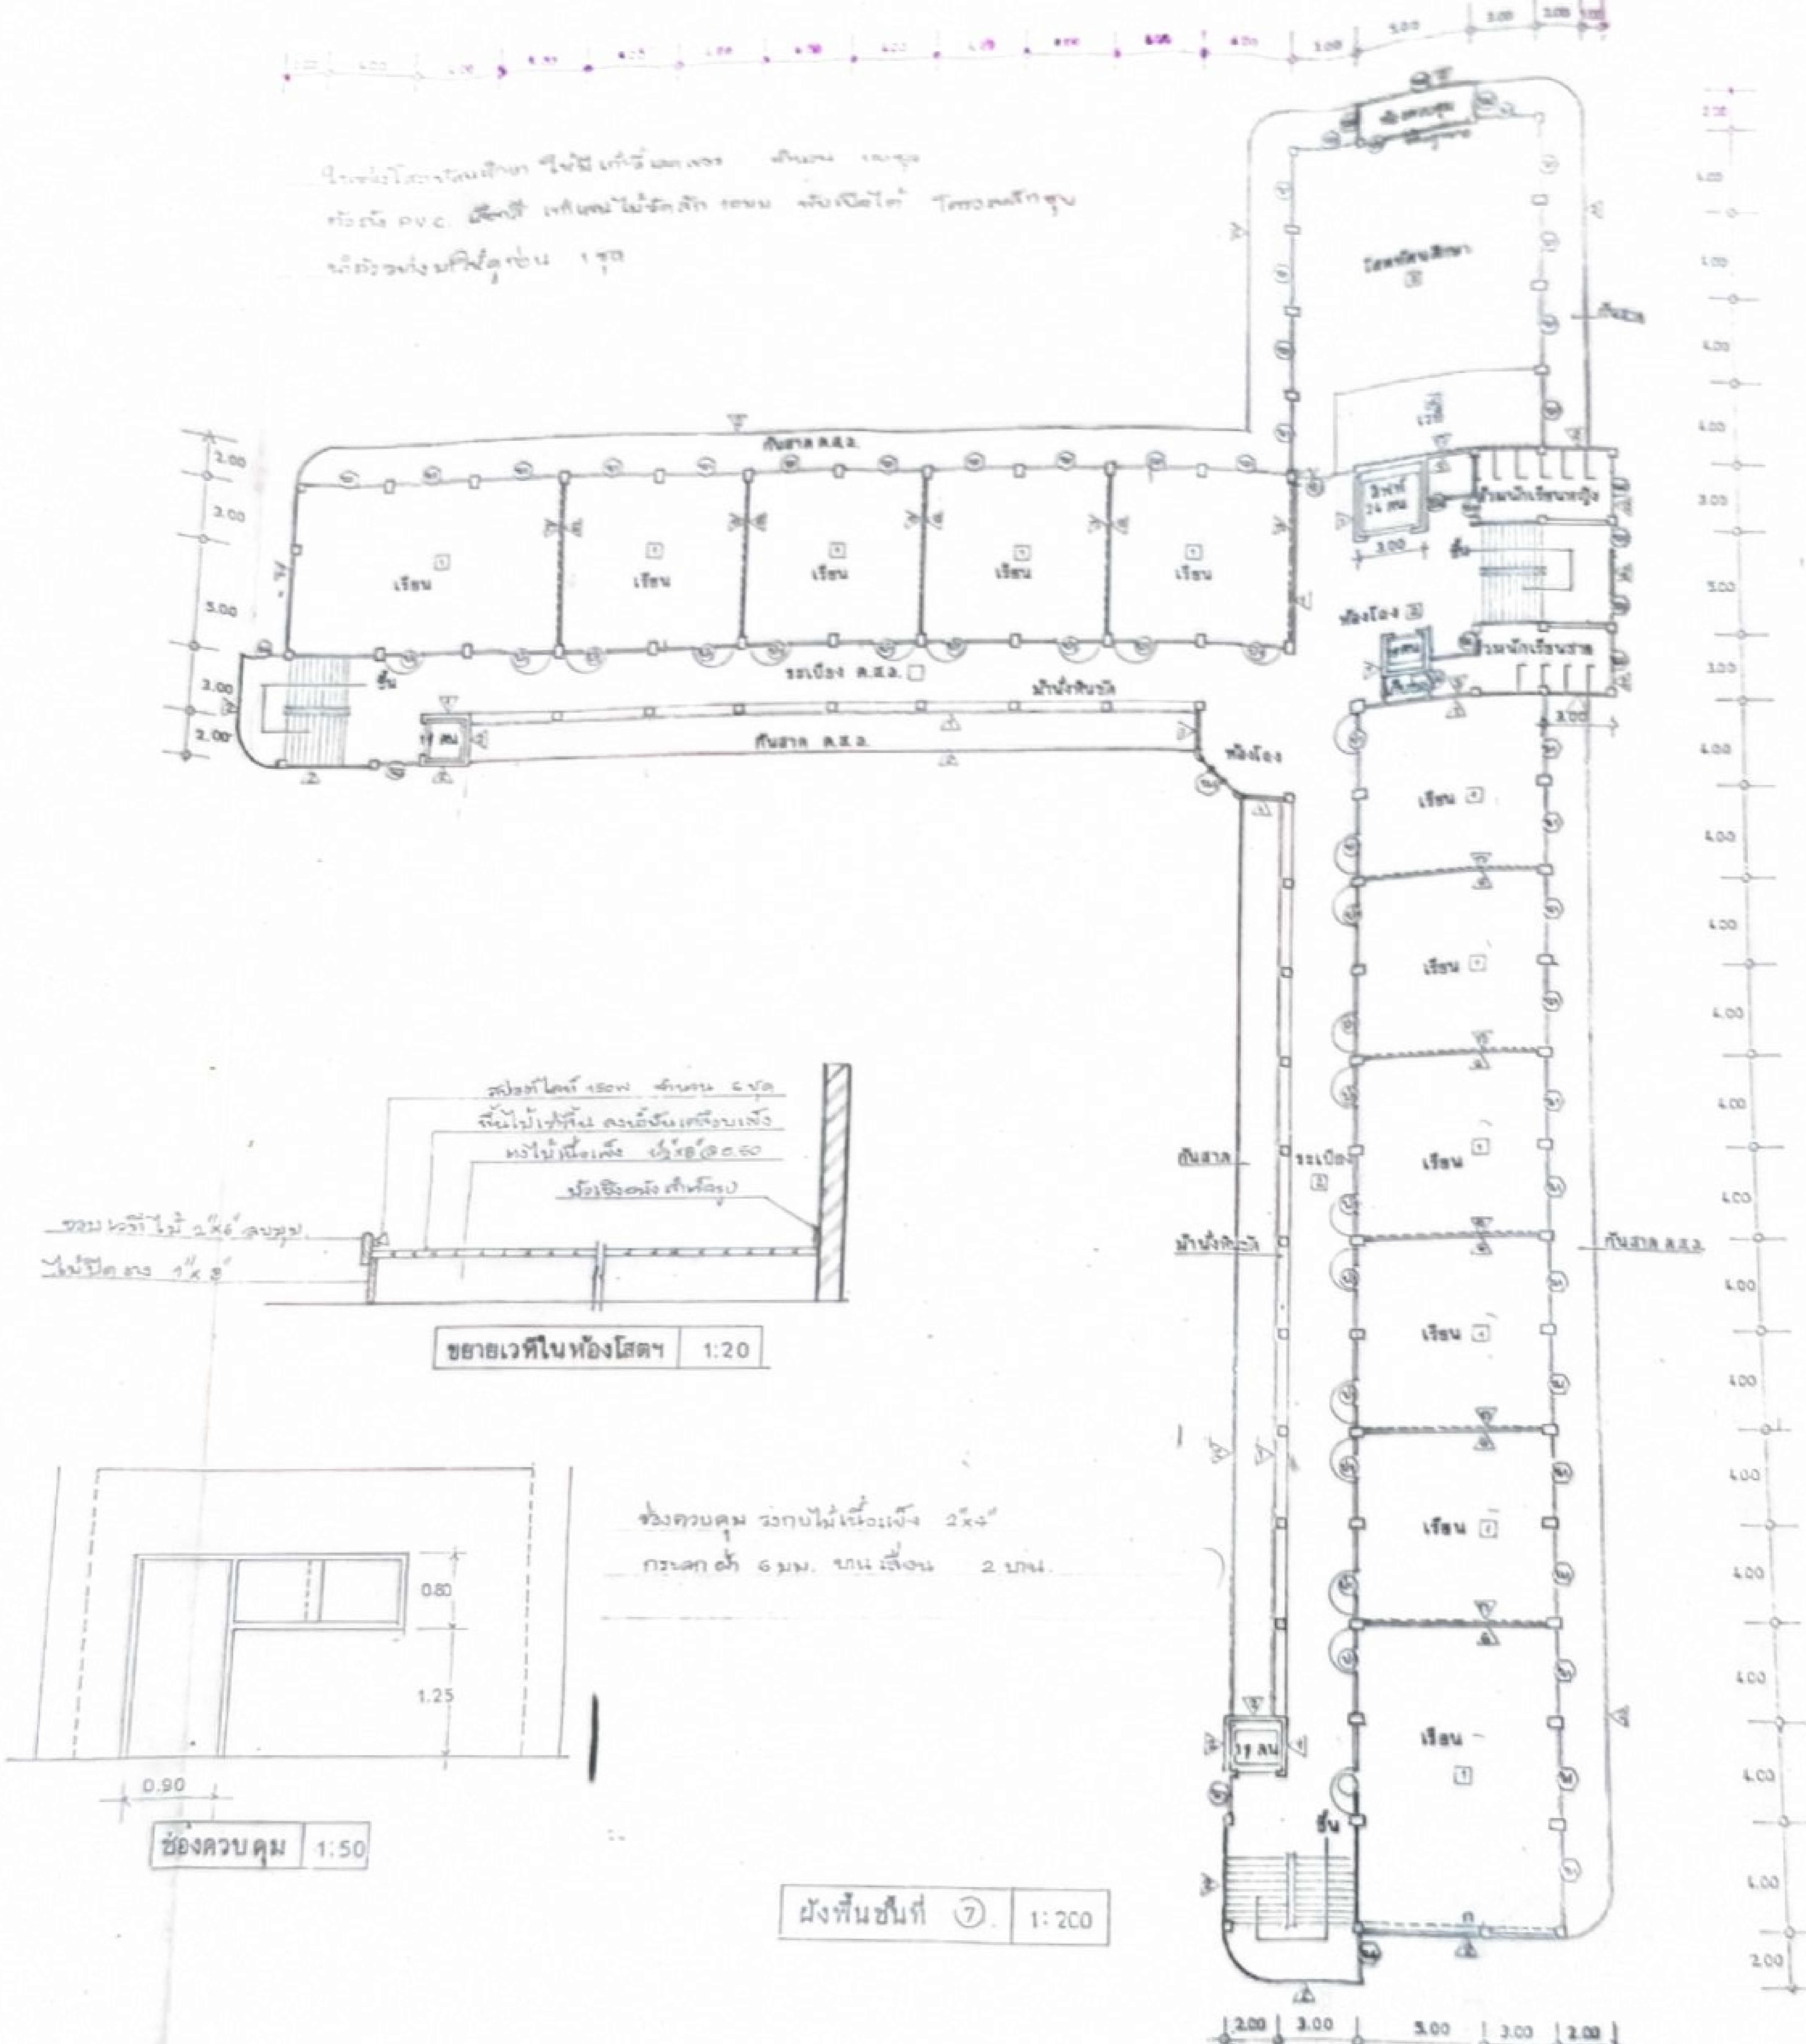
เรียน
เรียน
เรียน
เรียน
เรียน
เรียน
เรียน
เรียน
เรียน
เรียน
เรียน
โสตทัศนศึกษา
ห้องควบคุม
ห้องน้ำนักเรียนหญิง
ห้องน้ำนักเรียนชาย
ลิฟท์ 24 คน
15 คน
ห้องโถง
ขึ้น
ขึ้น
กันสาด ค.ส.ล.
กันสาด ค.ส.ล.
กันสาด ค.ส.ล.
กันสาด
ระเบียง ค.ส.ล.
ระเบียง
ม้านั่งหินขัด
ม้านั่งหินขัด
สปอตไลท์ 150W จำนวน 6 ชุด
พื้นไม้ปาร์เก้ ลงน้ำมันเคลือบเงา
ตงไม้เนื้อแข็ง 2"x6" @0.50
บัวเชิงผนัง ทำสีครอบ
ขอบเวทีไม้ 2"x6" ลบมุม
ไม้ปิดตง 1"x8"
0.80
1.25
0.90
2.00
3.00
5.00
4.00

ภายในห้องโสตทัศนศึกษา ใช้เก้าอี้เลคเชอร์ จำนวน [illegible] ชุด
หัวรับ PVC. สีครีม เคลือบผิวไม้สักสีทอง พับเปิดได้ โครงเหล็กชุบ
[illegible] 1 ชุด

ขยายเวทีในห้องโสตฯ 1:20

ช่องควบคุม วงกบไม้เนื้อแข็ง 2"x4"
กระจกดำ 6 มม. บานเลื่อน 2 บาน.

ช่องควบคุม 1:50

ผังพื้นชั้นที่ ⑦ 1:200

หมายเหตุ
ใช้สำหรับงานก่อสร้าง ของ
โรงเรียนสวนกุหลาบวิทยาลัย
ปี 2536

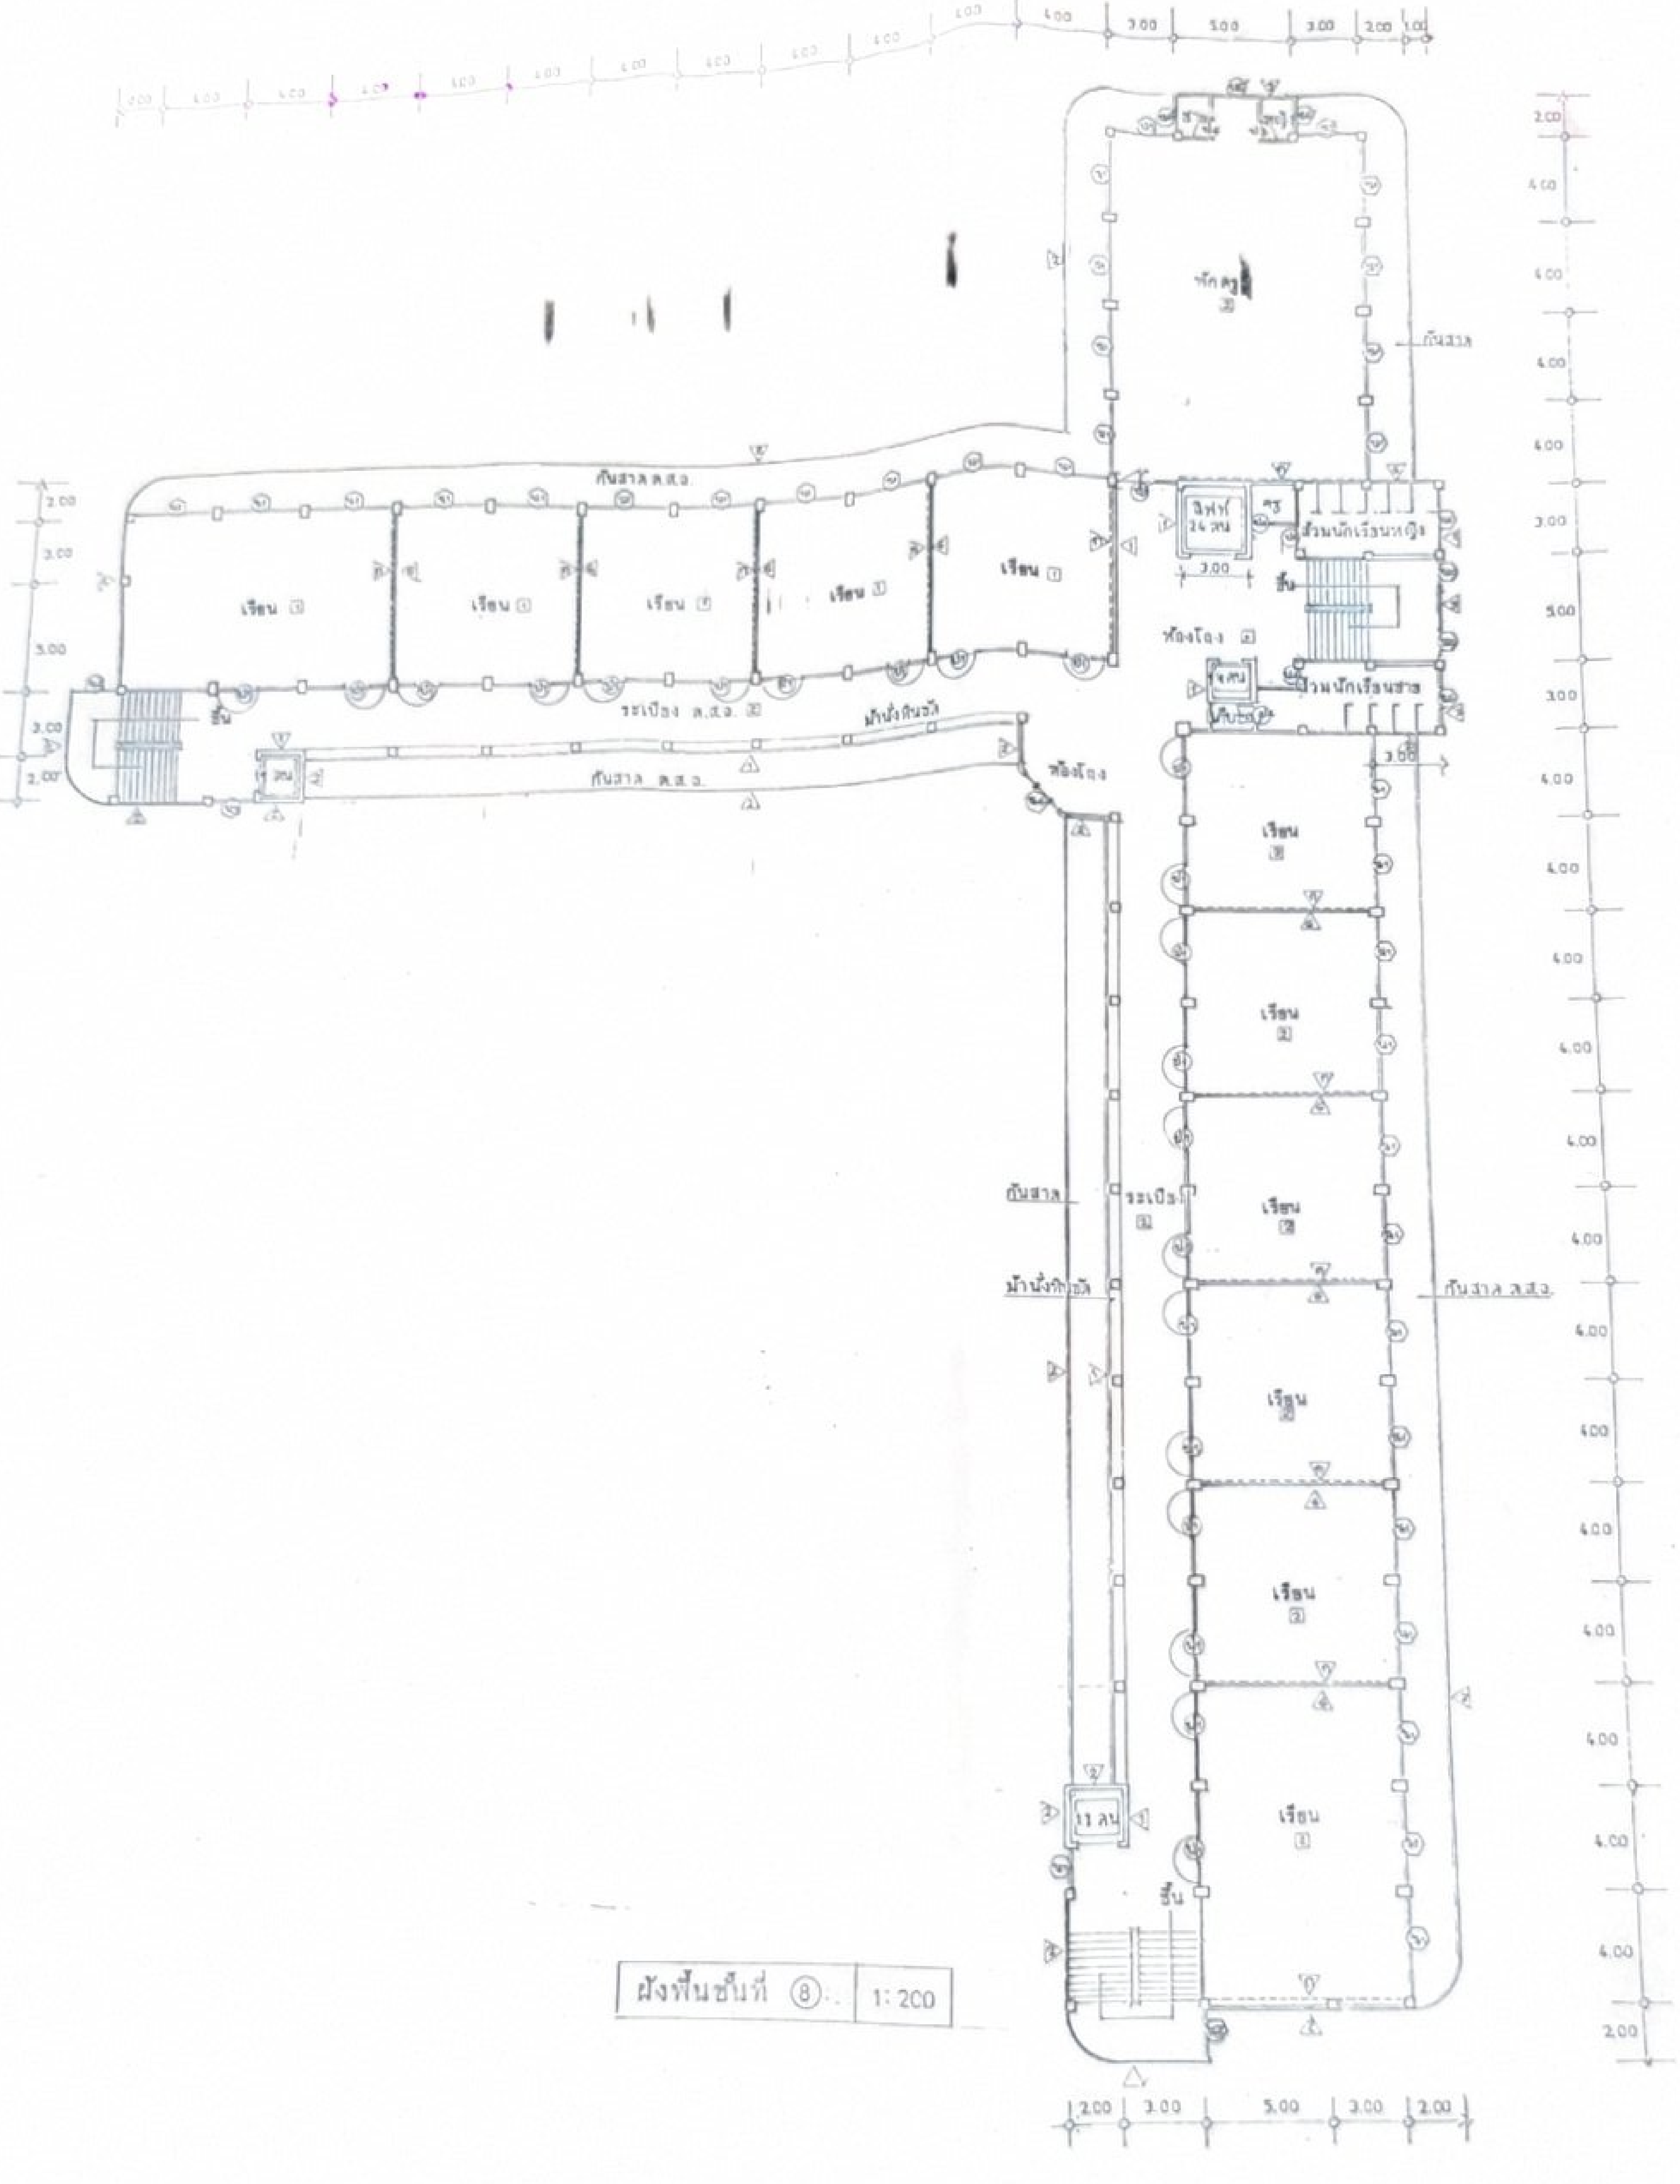
ห้องพักครู
กันสาด
ลิฟท์ 24 คน
ห้องน้ำนักเรียนหญิง
ขึ้น
ห้องโถง
ห้องน้ำนักเรียนชาย
3.00
เรียน
กันสาด ค.ส.ล.
ระเบียง ค.ส.ล.
ม้านั่งกันตก
ห้องโถง
ระเบียง
11 คน
2.00
3.00
4.00
5.00

ผังพื้นชั้นที่ ⑧ 1:200

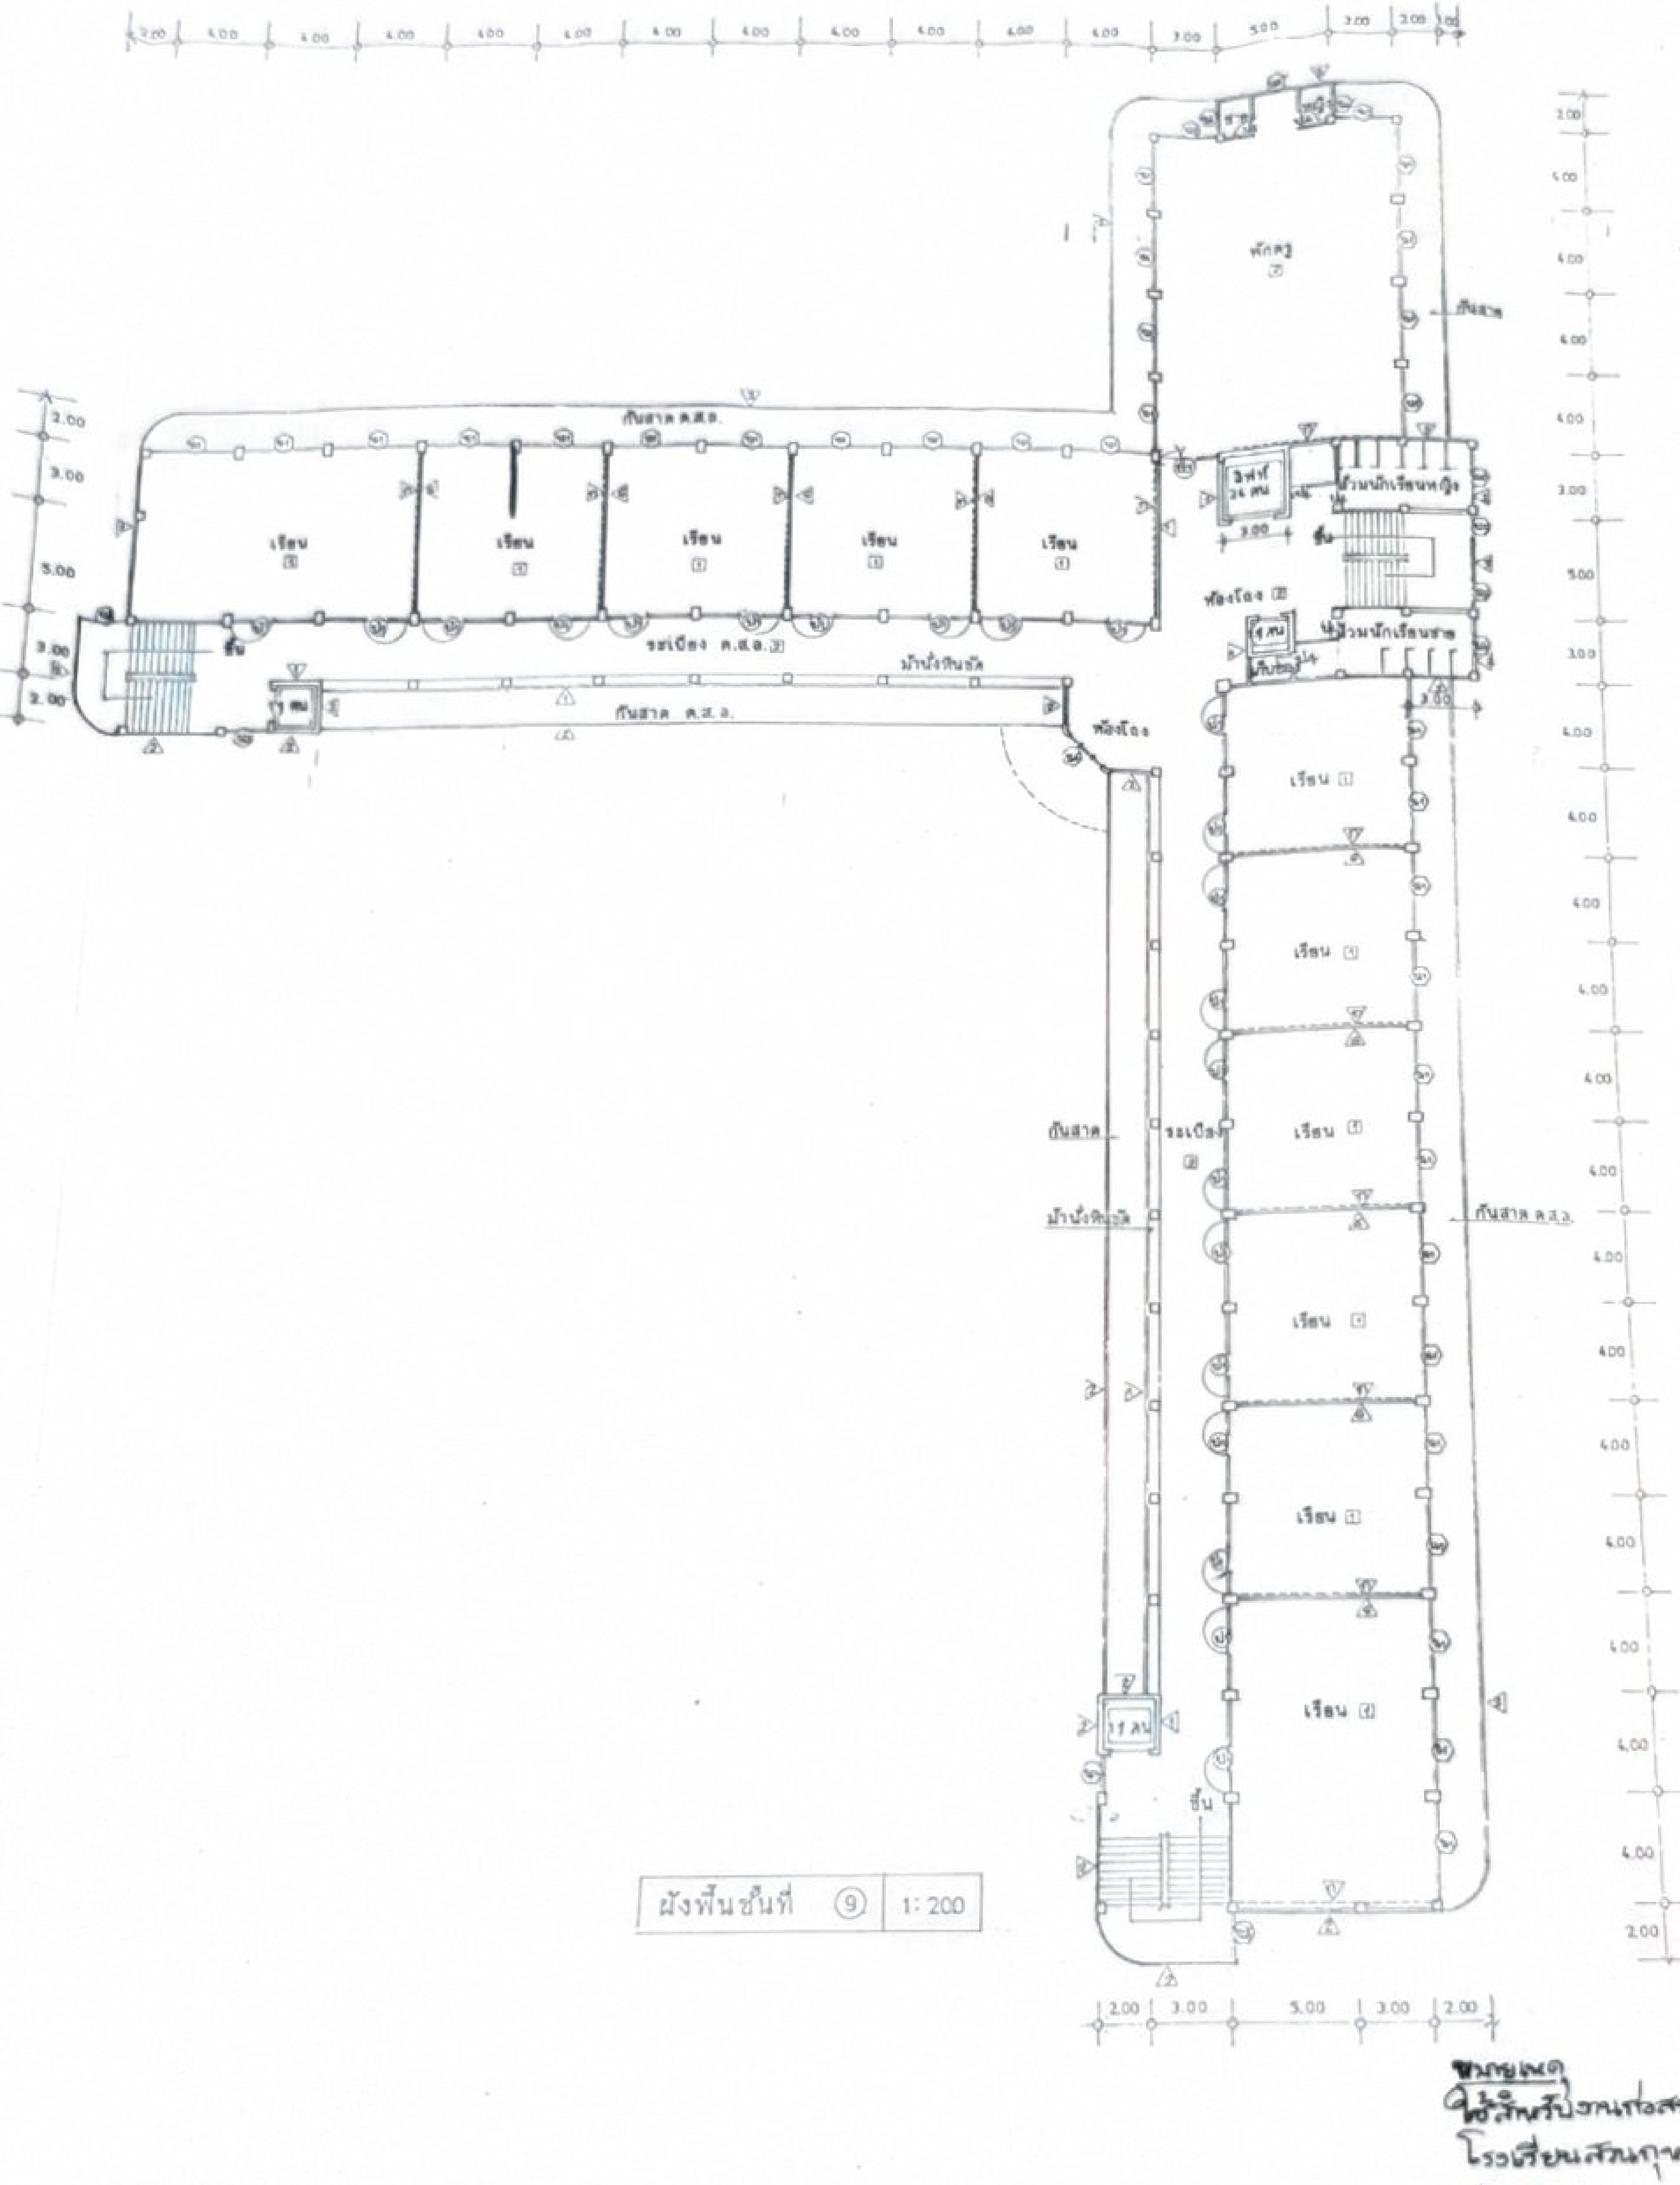
เรียน
พักครู
ลิฟท์ 26 คน
ห้องน้ำนักเรียนหญิง
ห้องน้ำนักเรียนชาย
ห้องโถง
ขึ้น
กันสาด ค.ส.ล.
ระเบียง ค.ส.ล.
ม้านั่งหินขัด
กันสาด
ระเบียง
2.00
3.00
4.00
5.00

ผังพื้นชั้นที่ ⑨ 1: 200

หมายเหตุ
ได้สิ้นสุดงานก่อสร้าง ของ
โรงเรียนสวนกุหลาบวิทยาลัย
ปี 2536

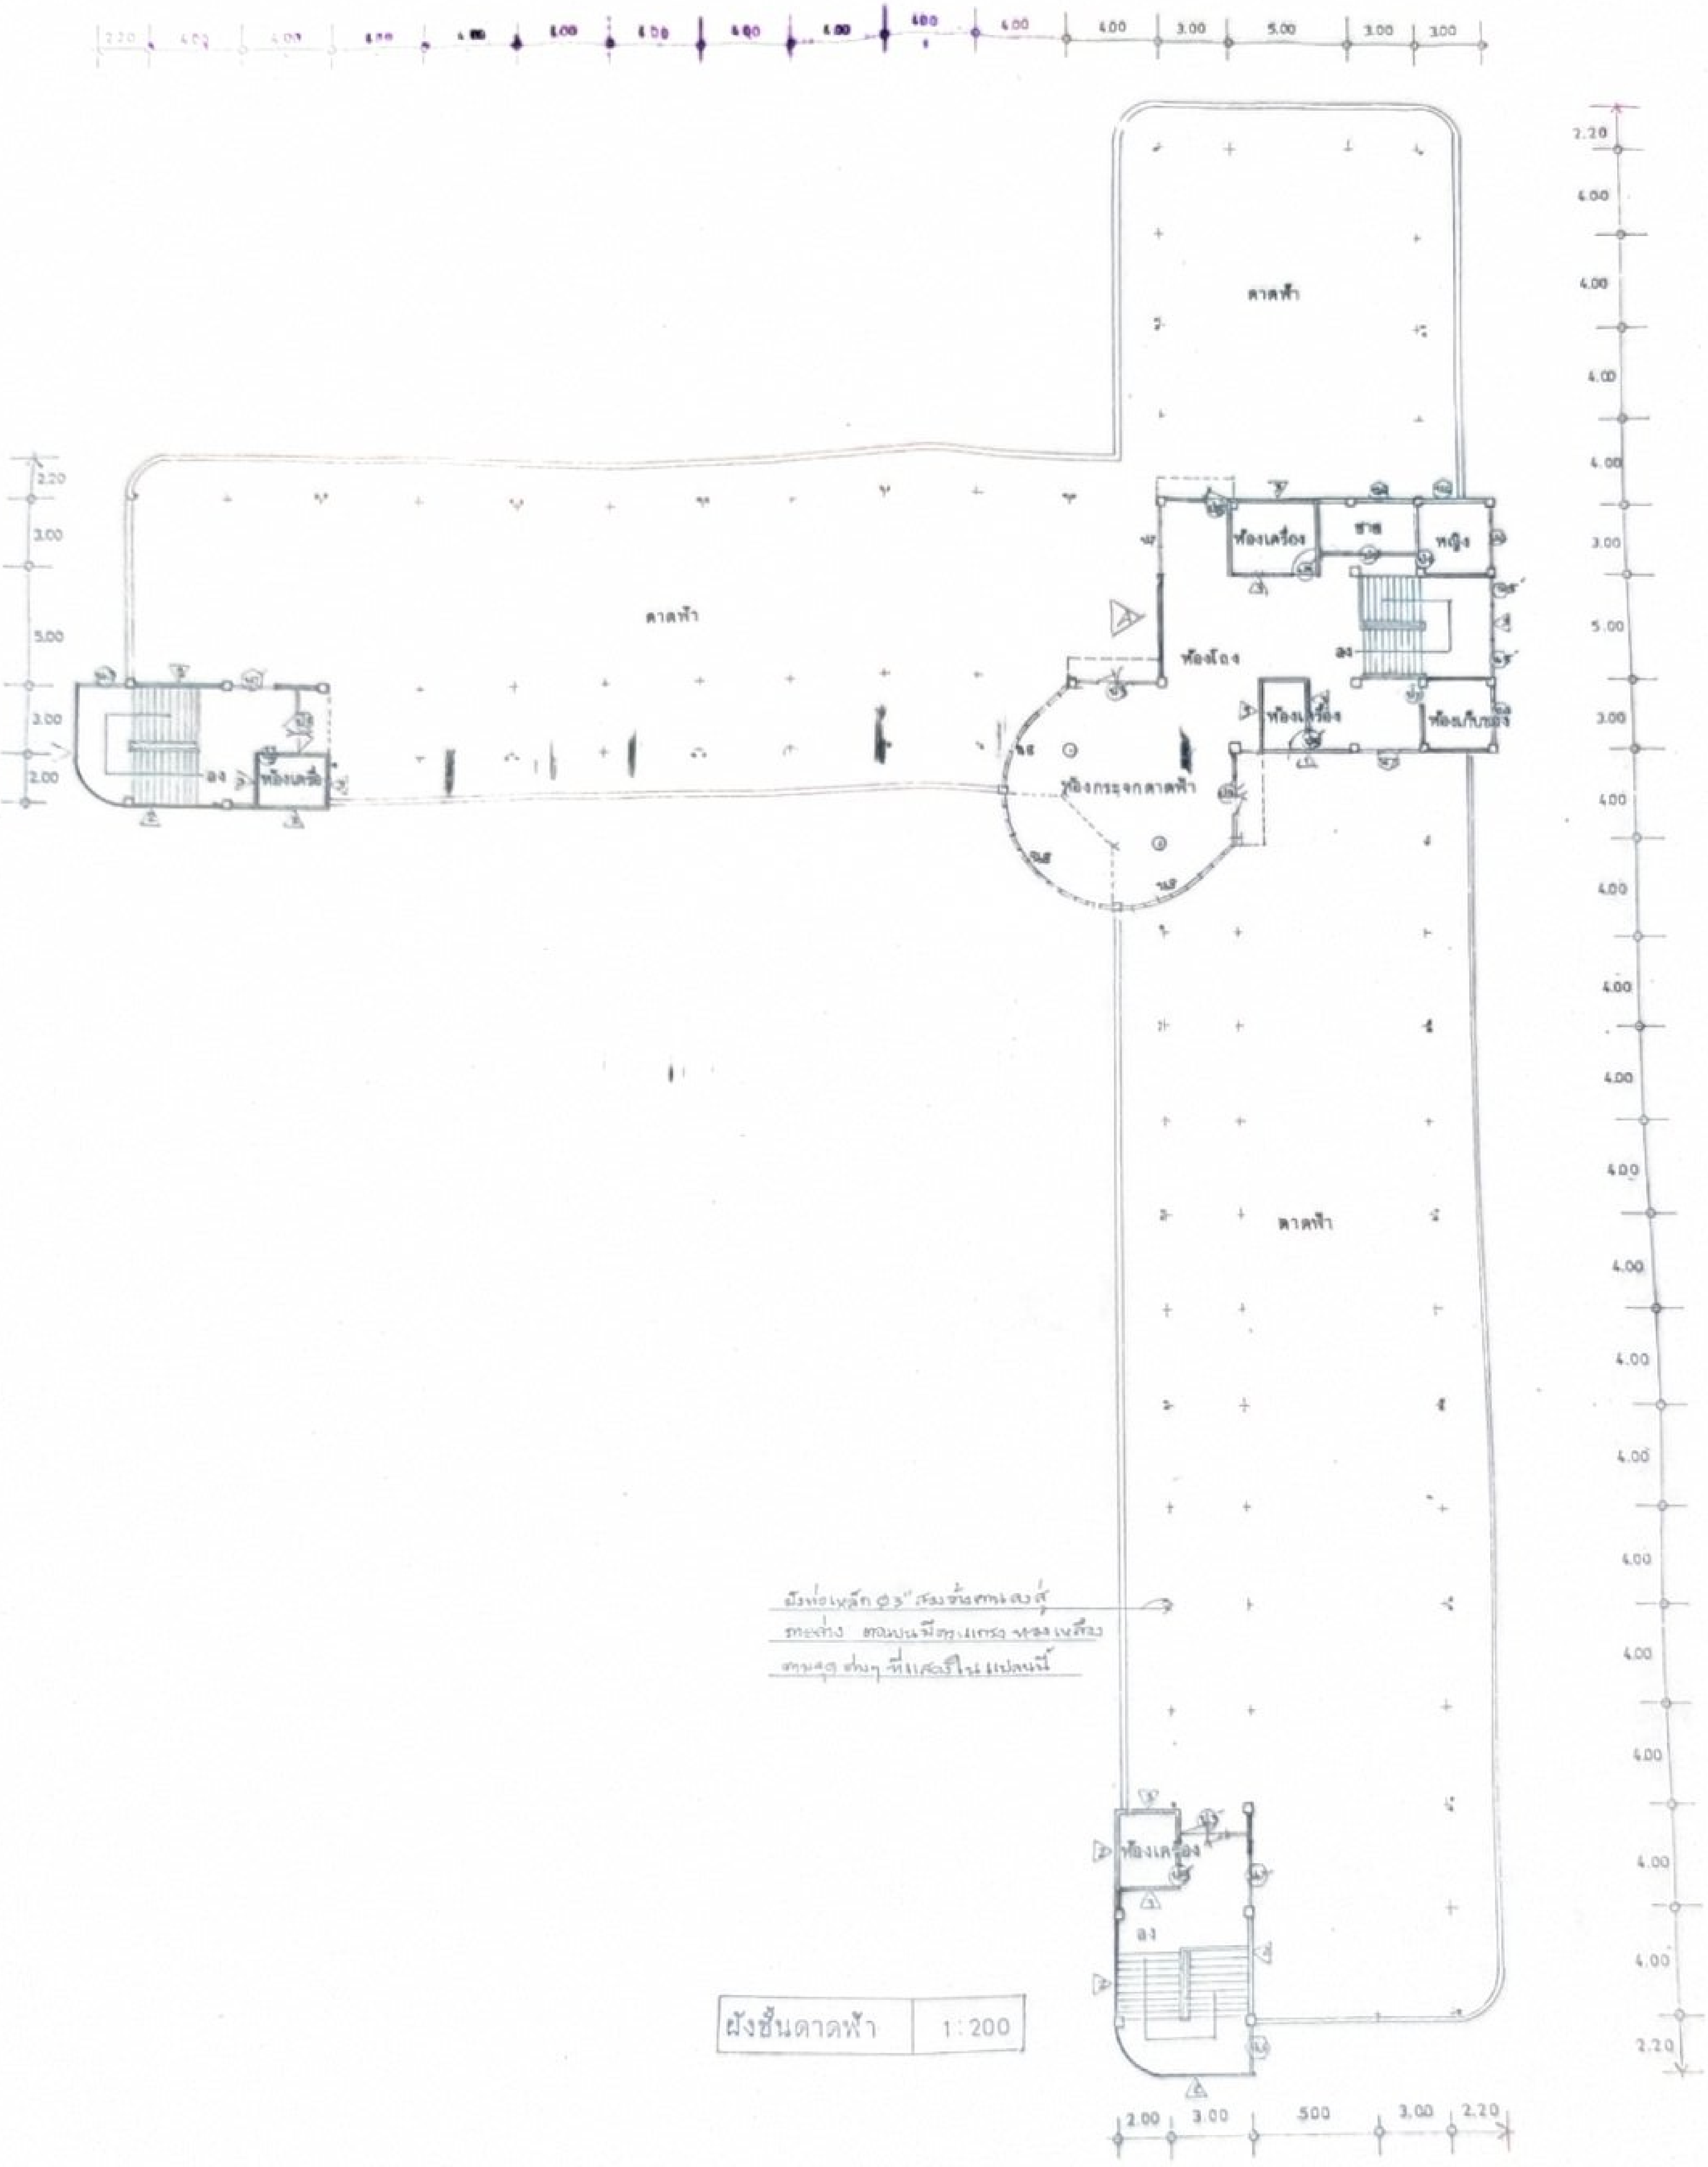
ดาดฟ้า
ดาดฟ้า
ดาดฟ้า
ห้องเครื่อง
ห้องเครื่อง
ห้องเครื่อง
ห้องเครื่อง
ชาย
หญิง
ห้องโถง
ห้องเก็บของ
ห้องกระจกดาดฟ้า
ลง
ลง
ลง
2.20
4.00
3.00
5.00
2.00

ฝังท่อเหล็ก Ø 3" ระบายน้ำฝนลงสู่
ท่อระบาย ตอนบนมีตะแกรง ทองเหลือง
ตามจุด ต่างๆ ที่แสดงไว้ในแปลนนี้

ผังชั้นดาดฟ้า 1:200

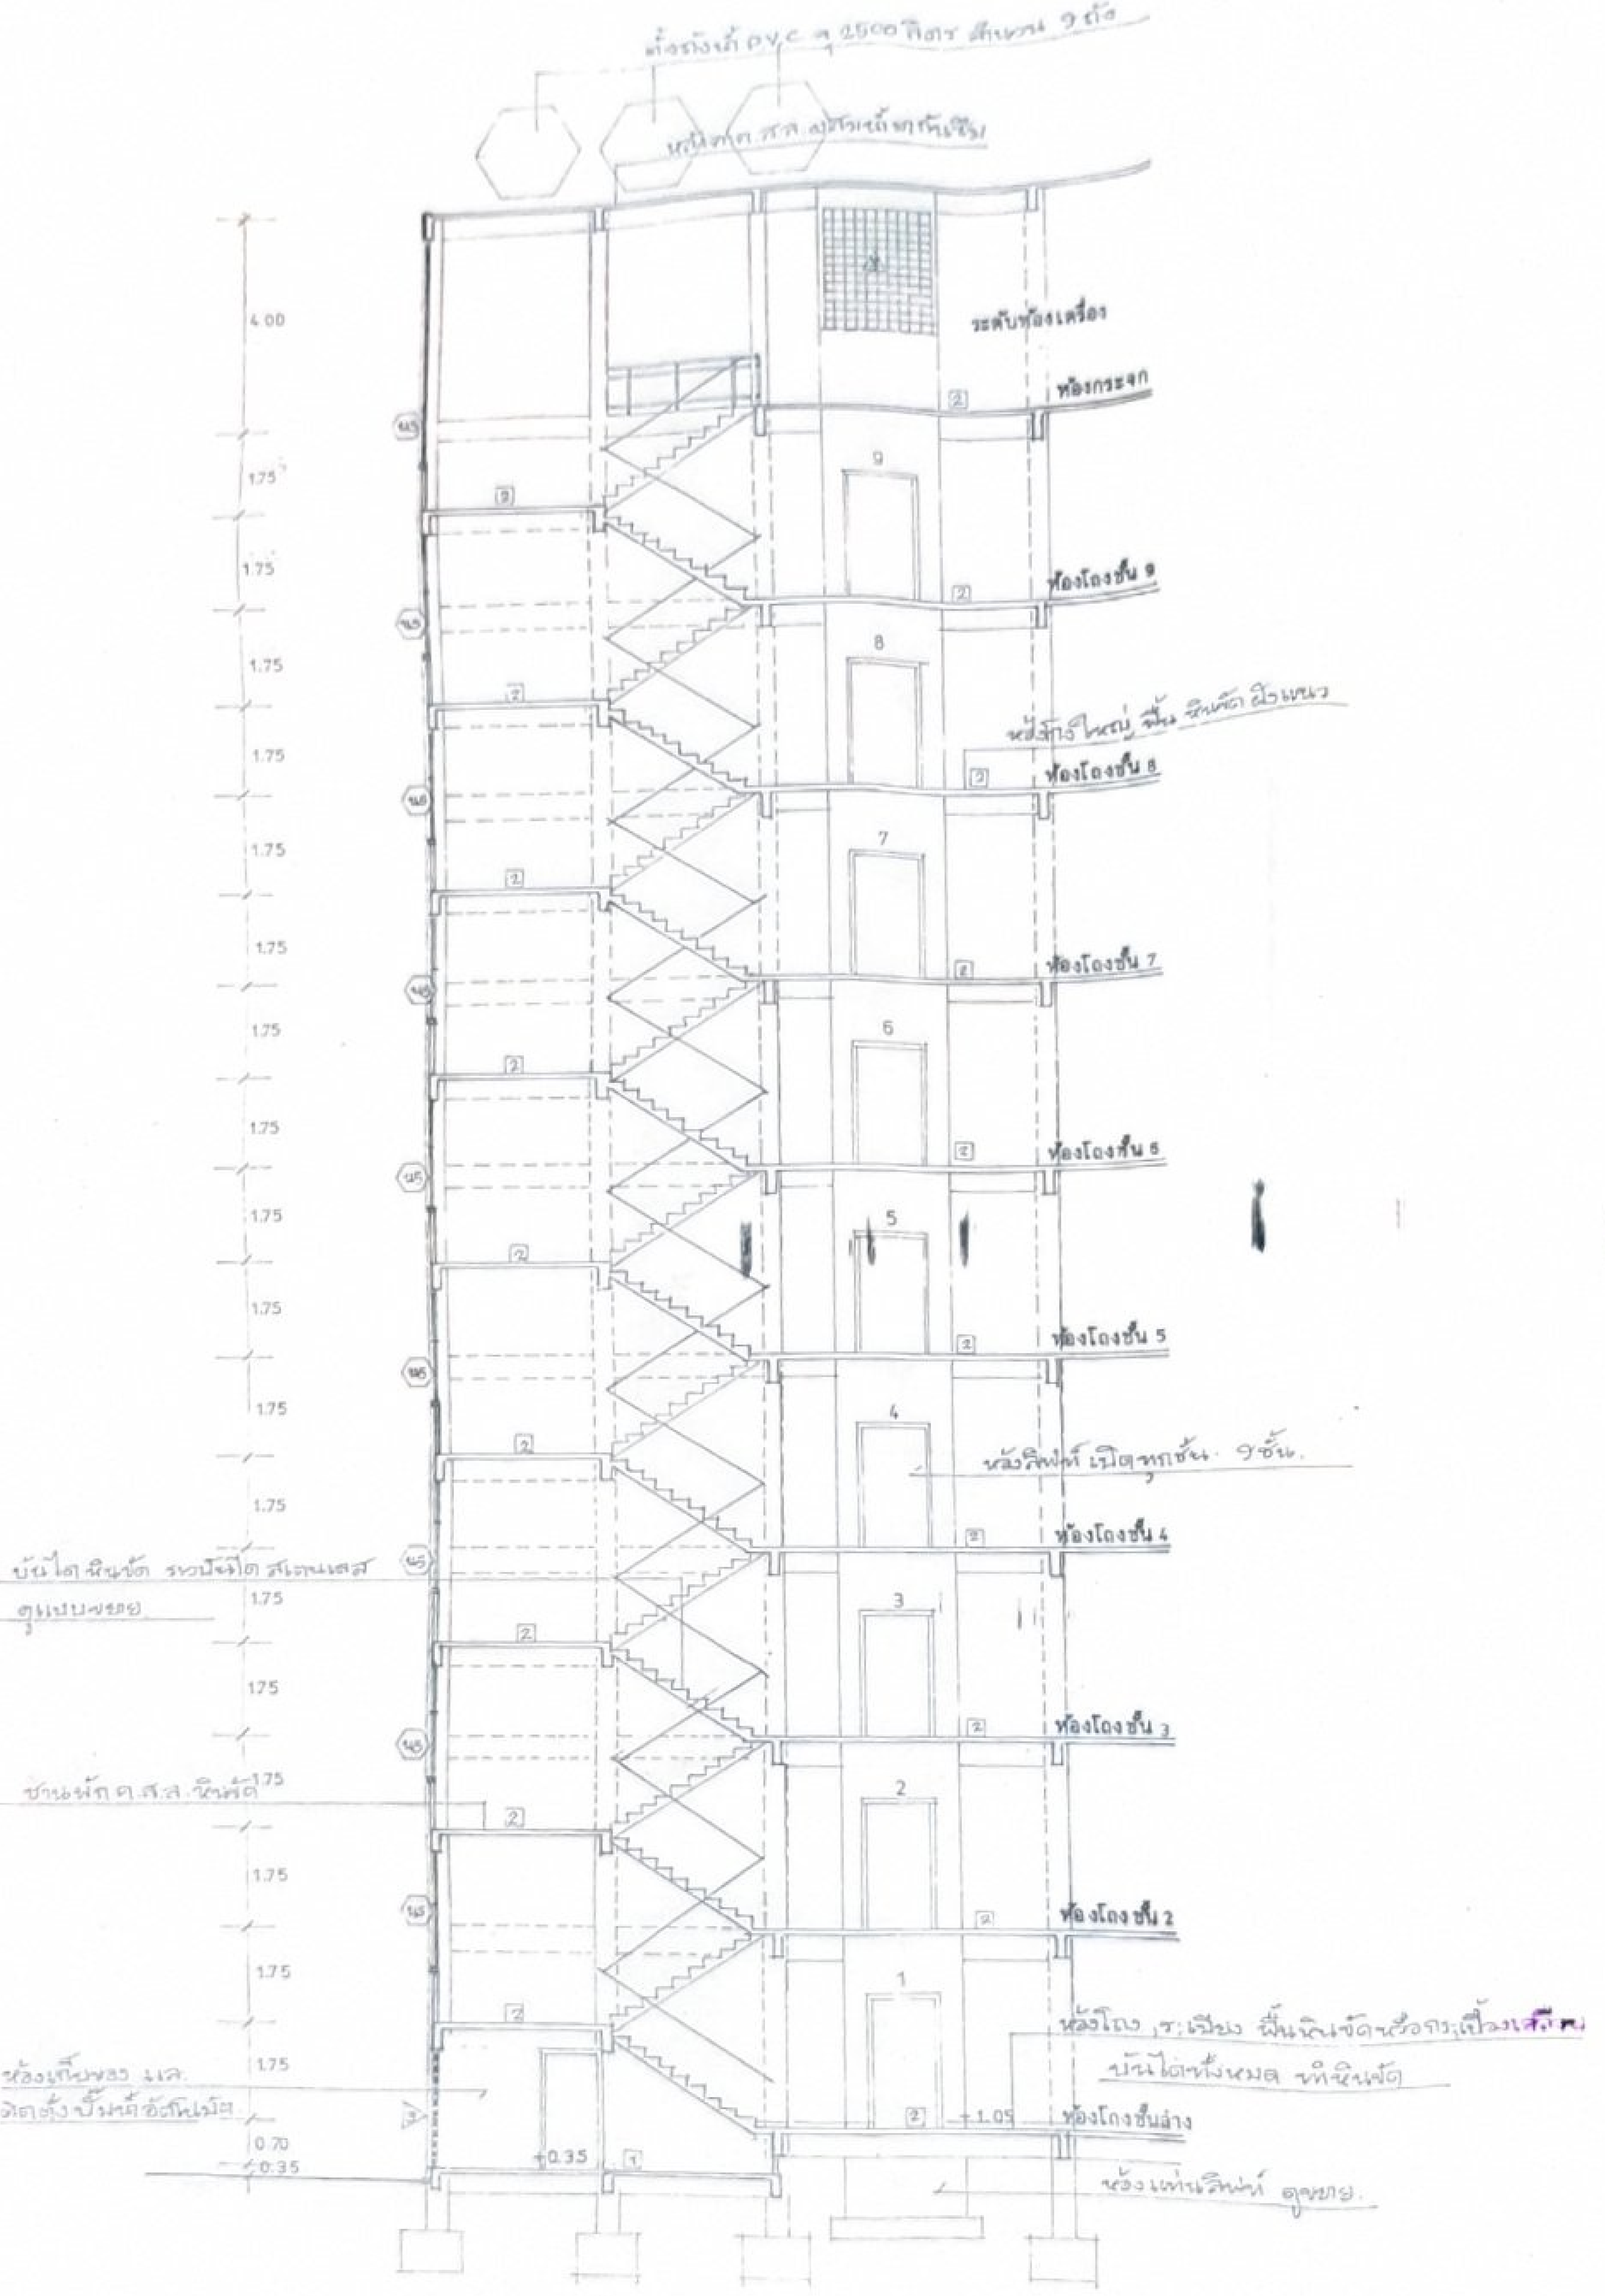
ถังรับน้ำ P.V.C จุ 2500 ลิตร จำนวน 9 ถัง
หลังคา ค.ส.ล. เสริมเหล็กทนไฟ
ระดับห้องเครื่อง
ห้องกระจก
9
ห้องโถงชั้น 9
8
ห้องโถงใหญ่ พื้น หินขัด ผิวเรียบ
ห้องโถงชั้น 8
7
ห้องโถงชั้น 7
6
ห้องโถงชั้น 6
5
ห้องโถงชั้น 5
4
ห้องลิฟท์ เปิดทุกชั้น 9ชั้น
ห้องโถงชั้น 4
3
ห้องโถงชั้น 3
2
ห้องโถงชั้น 2
1
ห้องโถง ระเบียง พื้นหินขัดหรือกระเบื้องเคลือบ
บันไดทั้งหมด ทำหินขัด
+1.05
ห้องโถงชั้นล่าง
ห้องแท่นลิฟท์ ดูขยาย
บันไดหินขัด ราวบันได สแตนเลส
ดูแบบขยาย
ชานพัก ค.ส.ล. หินขัด
ห้องเก็บของ และ
ติดตั้งปั๊มน้ำอัตโนมัติ
4.00
1.75
0.70
0.35
+0.35
3.00
3.00
5.00

รูปตัด ⓧ-ⓧ 1:100